
VECTORWORKS EDUCATIONAL VERSION

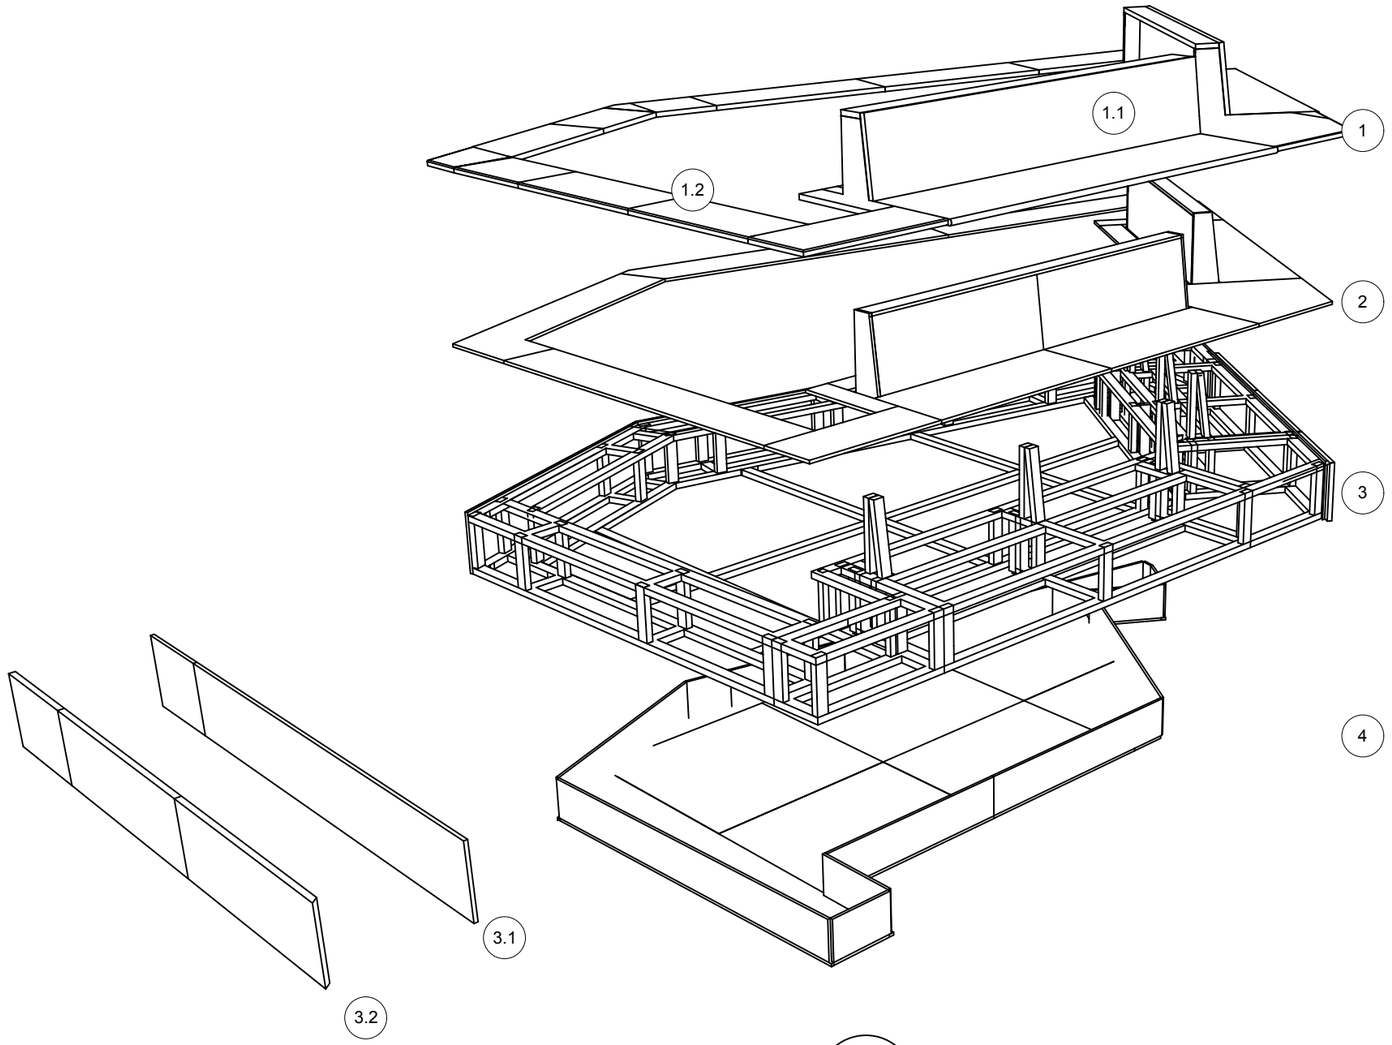

1 Exploded view
Schaal: 1:50

1 Uiterlijk / bovenste laag van de bank

1.1 Gebeitst eikenhout platen
1x: 2500 x 550 x 30 mm (zit) afgeronde rand
1x: 2500 x 436 x 30 mm (rug)
1x: 1625 x 550 x 30 mm (zit) afgeronde rand
1x: 1625 x 436 x 30 mm (rug)

1.2 Hergebruikt Gepolijst Belgisch Hardsteen, afgeronde hoeken
('t Achterhuis Historische bouwmaterialen bv)
9x: 600 x 300 x 30 mm
5x: 600 x 600 x 30 mm
5x: 900 x 900 x 30 mm
5x: 600 x 1200 x 30 mm

2 Vuren multiplex
4x: Fins vuren multiplex II/III TG2 FSC
2440 x 1220 x 18 mm

3 Frame
Vuren LVL T-Grade 39x69x2700mm 70% PEFC - Bouwmaat.nl

3.1 Vuren multiplex
Fins vuren multiplex II/III TG2 FSC
2440 x 1220 x 18 mm

3.2 Hergebruikt Gepolijst Belgisch Hardsteen, afgeronde hoeken
('t Achterhuis Historische bouwmaterialen bv)
4x: 600 x 300 x 30 mm
2x: 600 x 600 x 30 mm
7x: 900 x 900 x 30 mm
2x: 600 x 1200 x 30 mm

4 Plantenbak
Vuren multiplex
6x: Fins vuren multiplex II/III TG2 FSC
2440 x 1220 x 18 mm
EPDM-folie

GUUSJE ROZENDOM
GUUSJE@GMAIL.COM
PROJECTMATIG INTERIEUR ONTWERP

Ontwerp: Afstudeeropdracht Deventer Ziekenhuis - Maatwerk technische tekening bank
Ontwerper: Guusje Rozendom
Opdrachtgever: Interior Design & Styling
Schaal: 1:50
Formaat: A3
Eenheid: mm
Datum: 19.01.2024
Tekening nr.: 3

VECTORWORKS EDUCATIONAL VERSION