


VECTORWORKS EDUCATIONAL VERSION

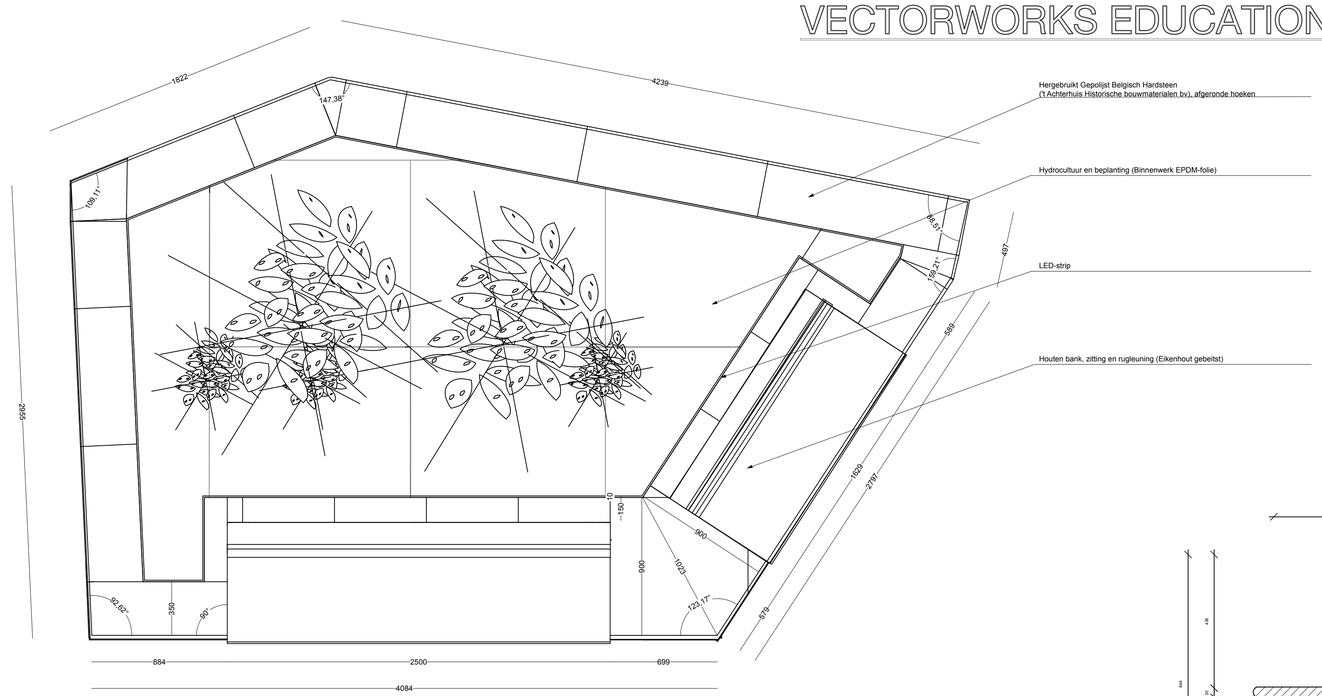

1 Bovenaanzicht Bank
Schaal: 1:20

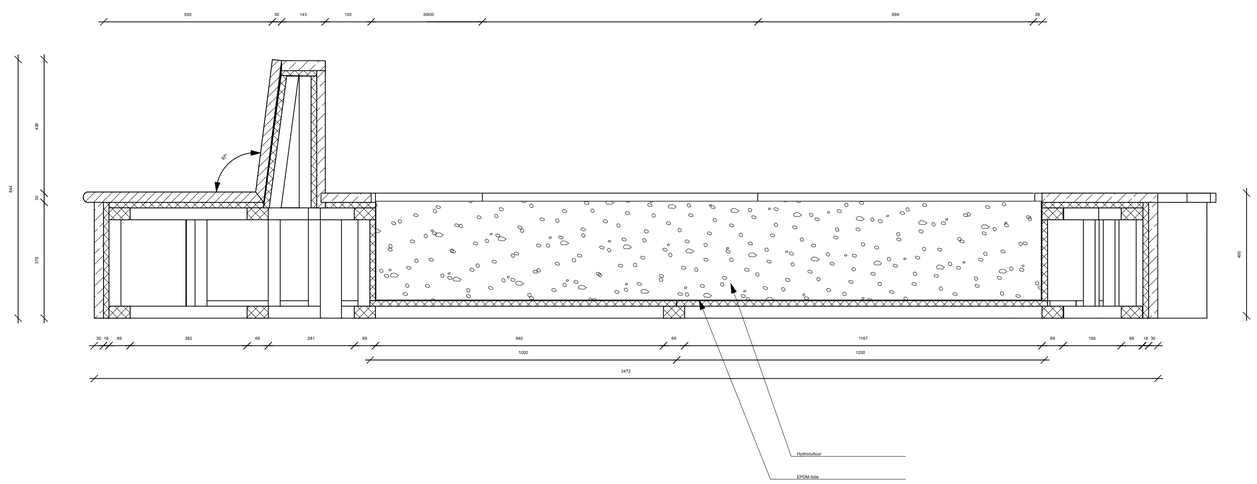

3 Dwarsdoorsnede
Schaal: 1:10

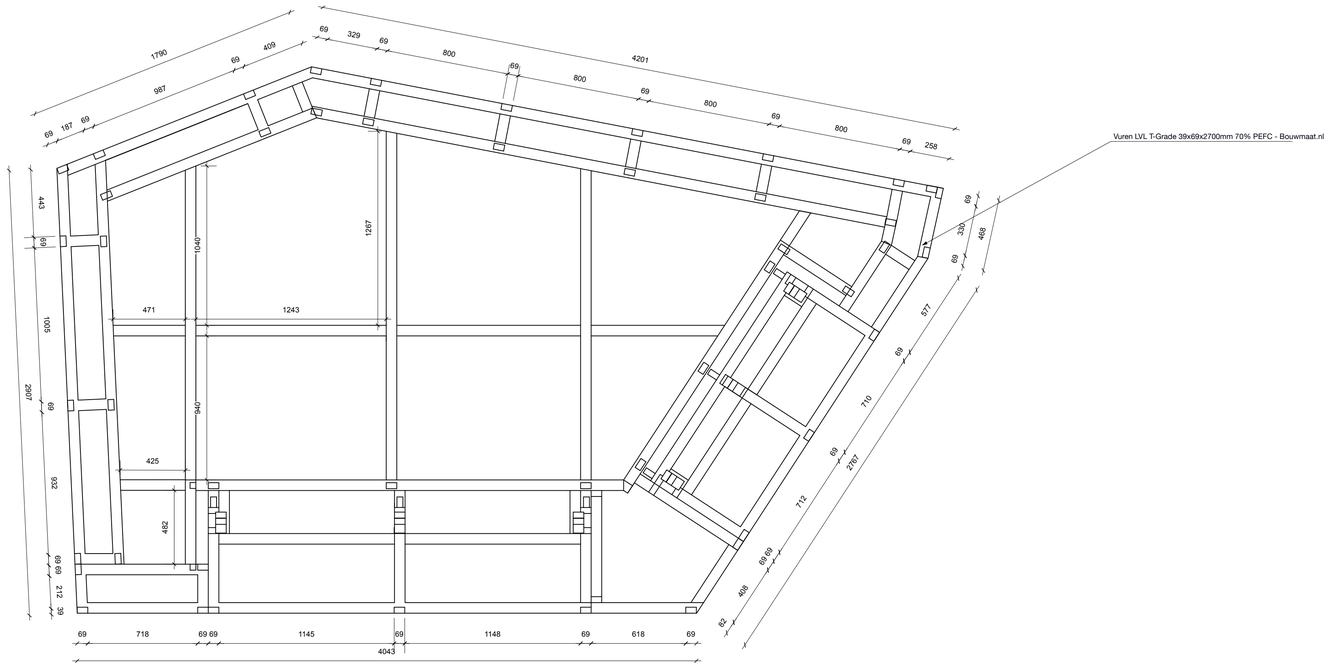

2 Bovenaanzicht Frame
Schaal: 1:20

	Hergebruikt Gepolijst Belgisch Hardsteen, afgeronde hoeken ('t Achterhuis Historische bouwmaterialen bv)
	Gebeitst eikenhout platen
	Plaat: Fins vuren multiplex II/III TG2 FSC 2440 x 1220 x 18 mm Frame: Vuren LVL T-Grade 39x69x2700mm 70% PEFC Bouwmaat.nl
	Hydrocultuur
	EPDM-Folie

GUUSJE ROZENDOM
GUUSJE@GMAIL.COM
PROJECTMATIG INTERIEUR ONTWERP

Ontwerp:	Afstudeeropdracht Deventer Ziekenhuis - Maatwerk technische tekening bank
Ontwerper:	Guusje Rozendom
Opdrachtgever:	Interior Design & Styling
Schaal:	1:10, 1:20
Formaat:	A1
Eenheid:	mm
Datum:	19.01.2024
Tekening nr.	2

VECTORWORKS EDUCATIONAL VERSION