VECTORWORKS EDUCATIONAL VERSION

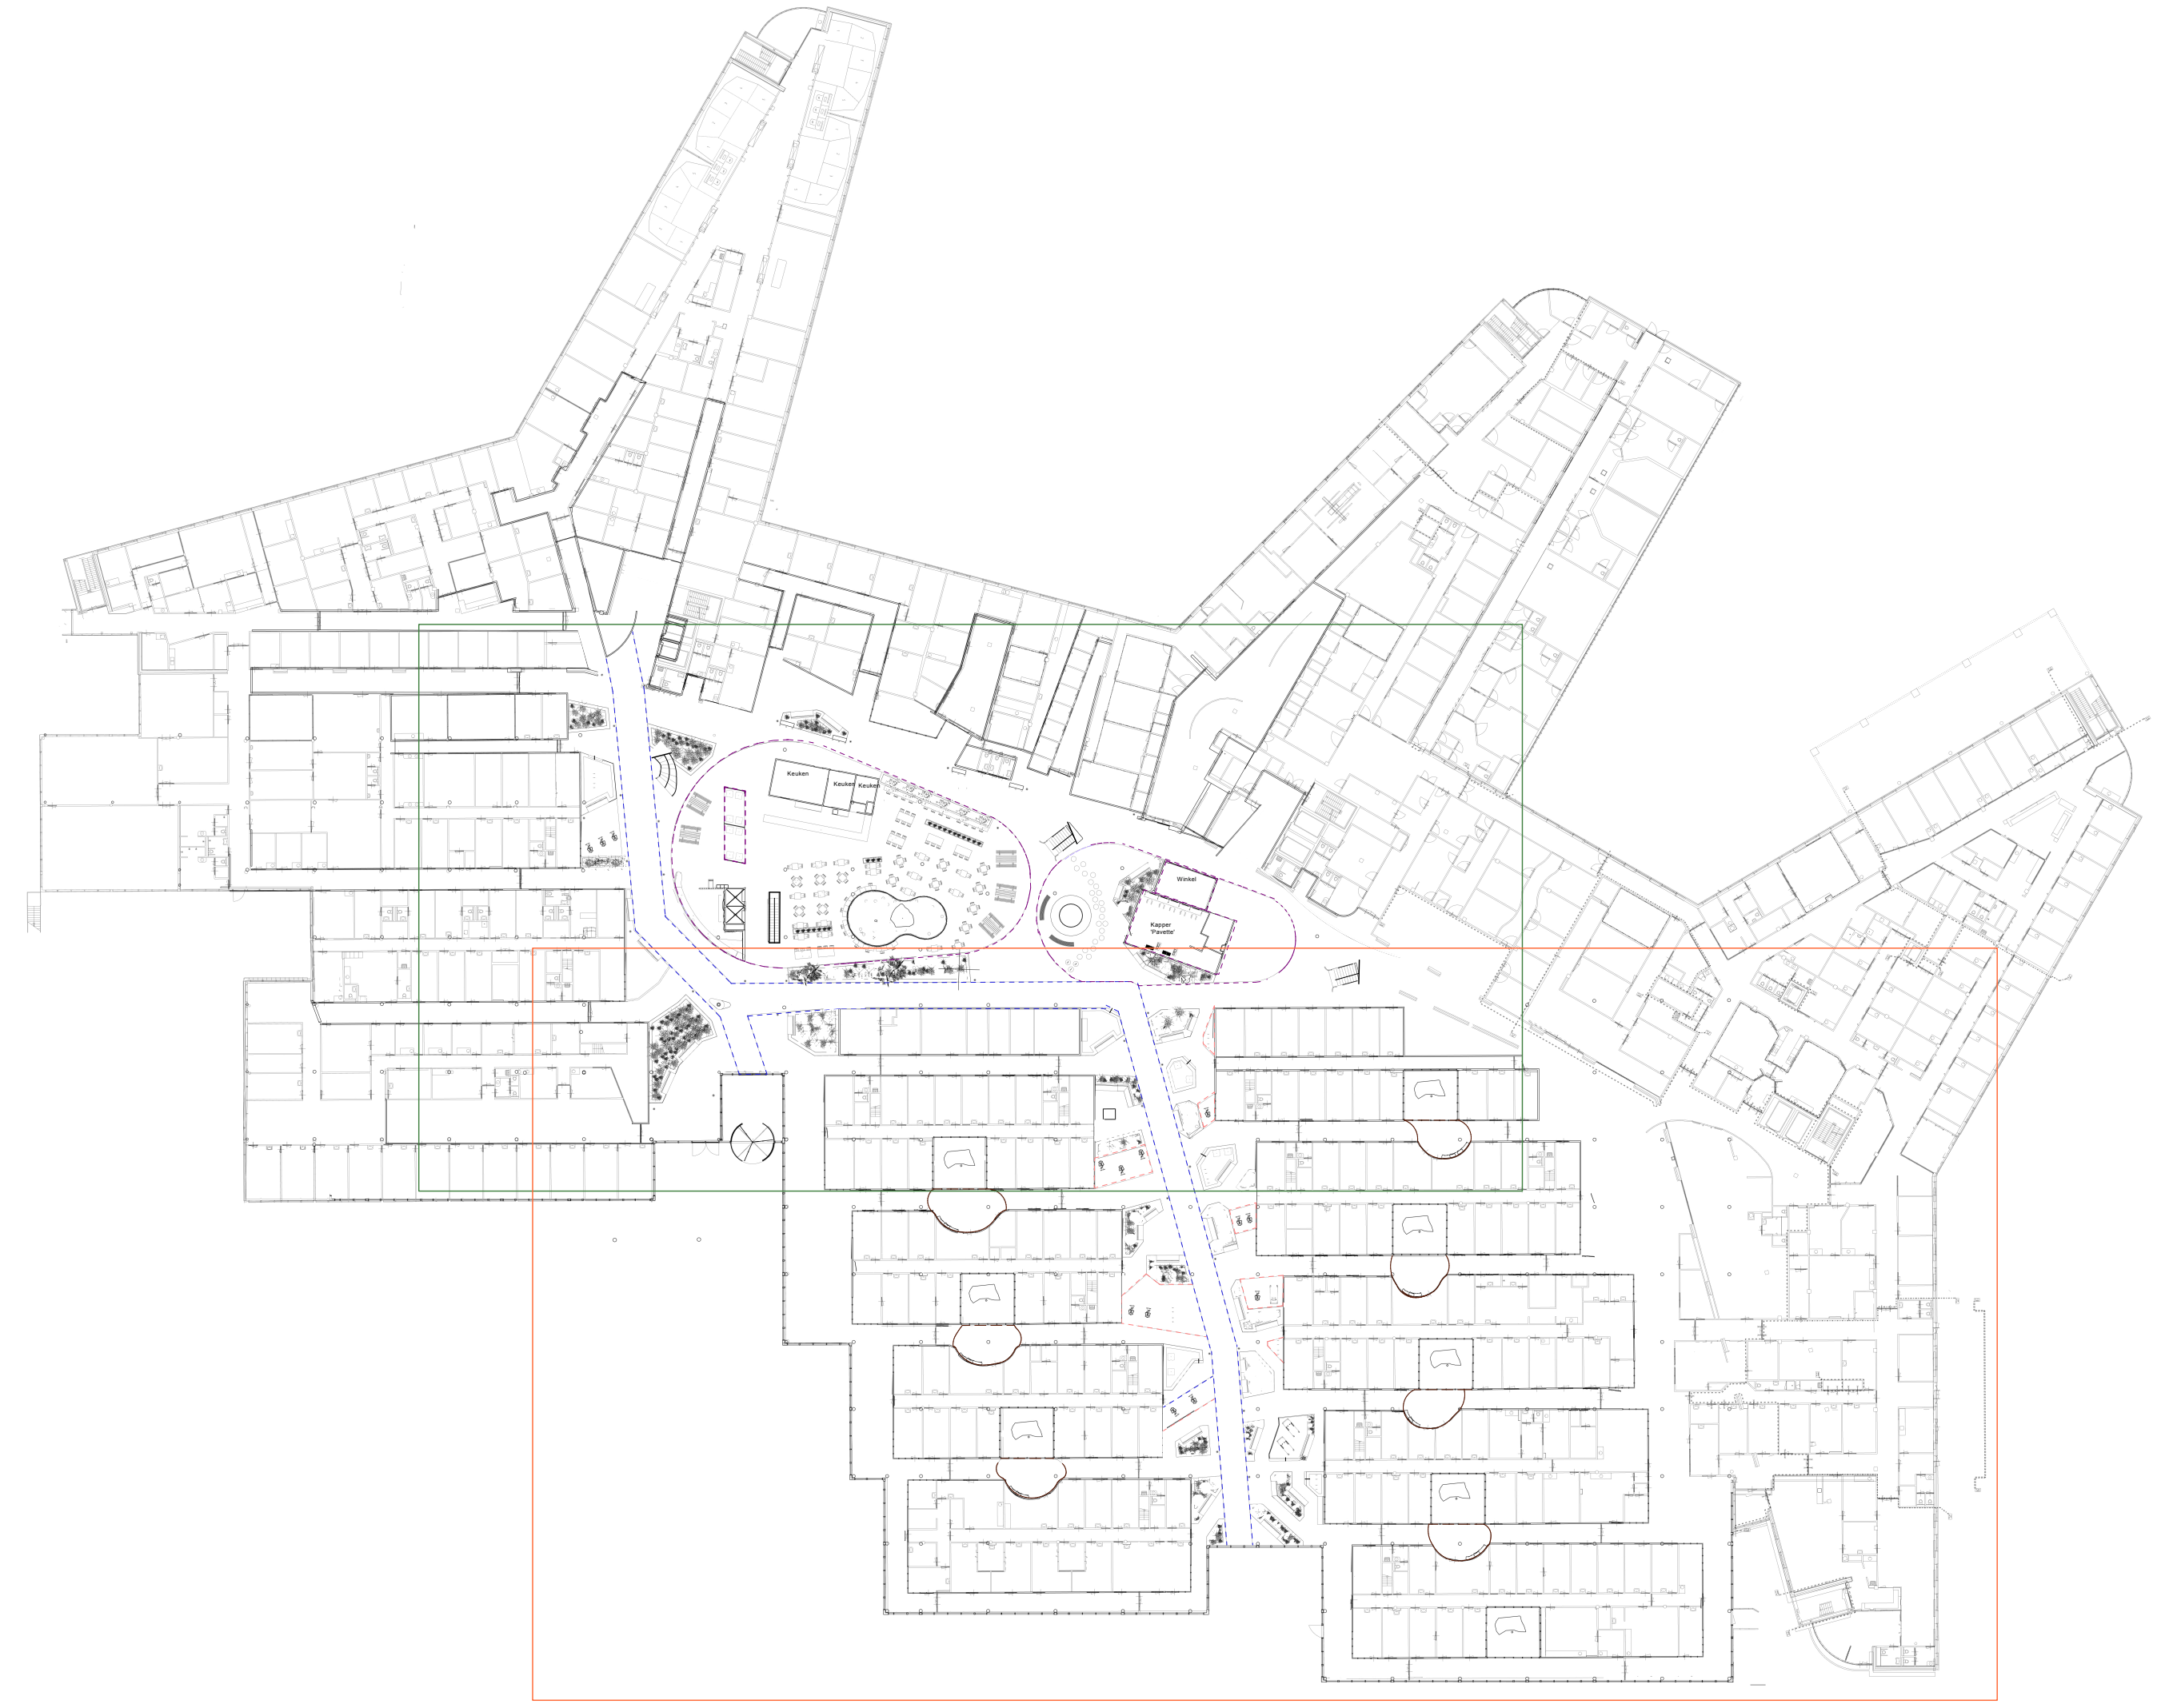

1 Volledige Plattegrond BG
Schaal: 1:500

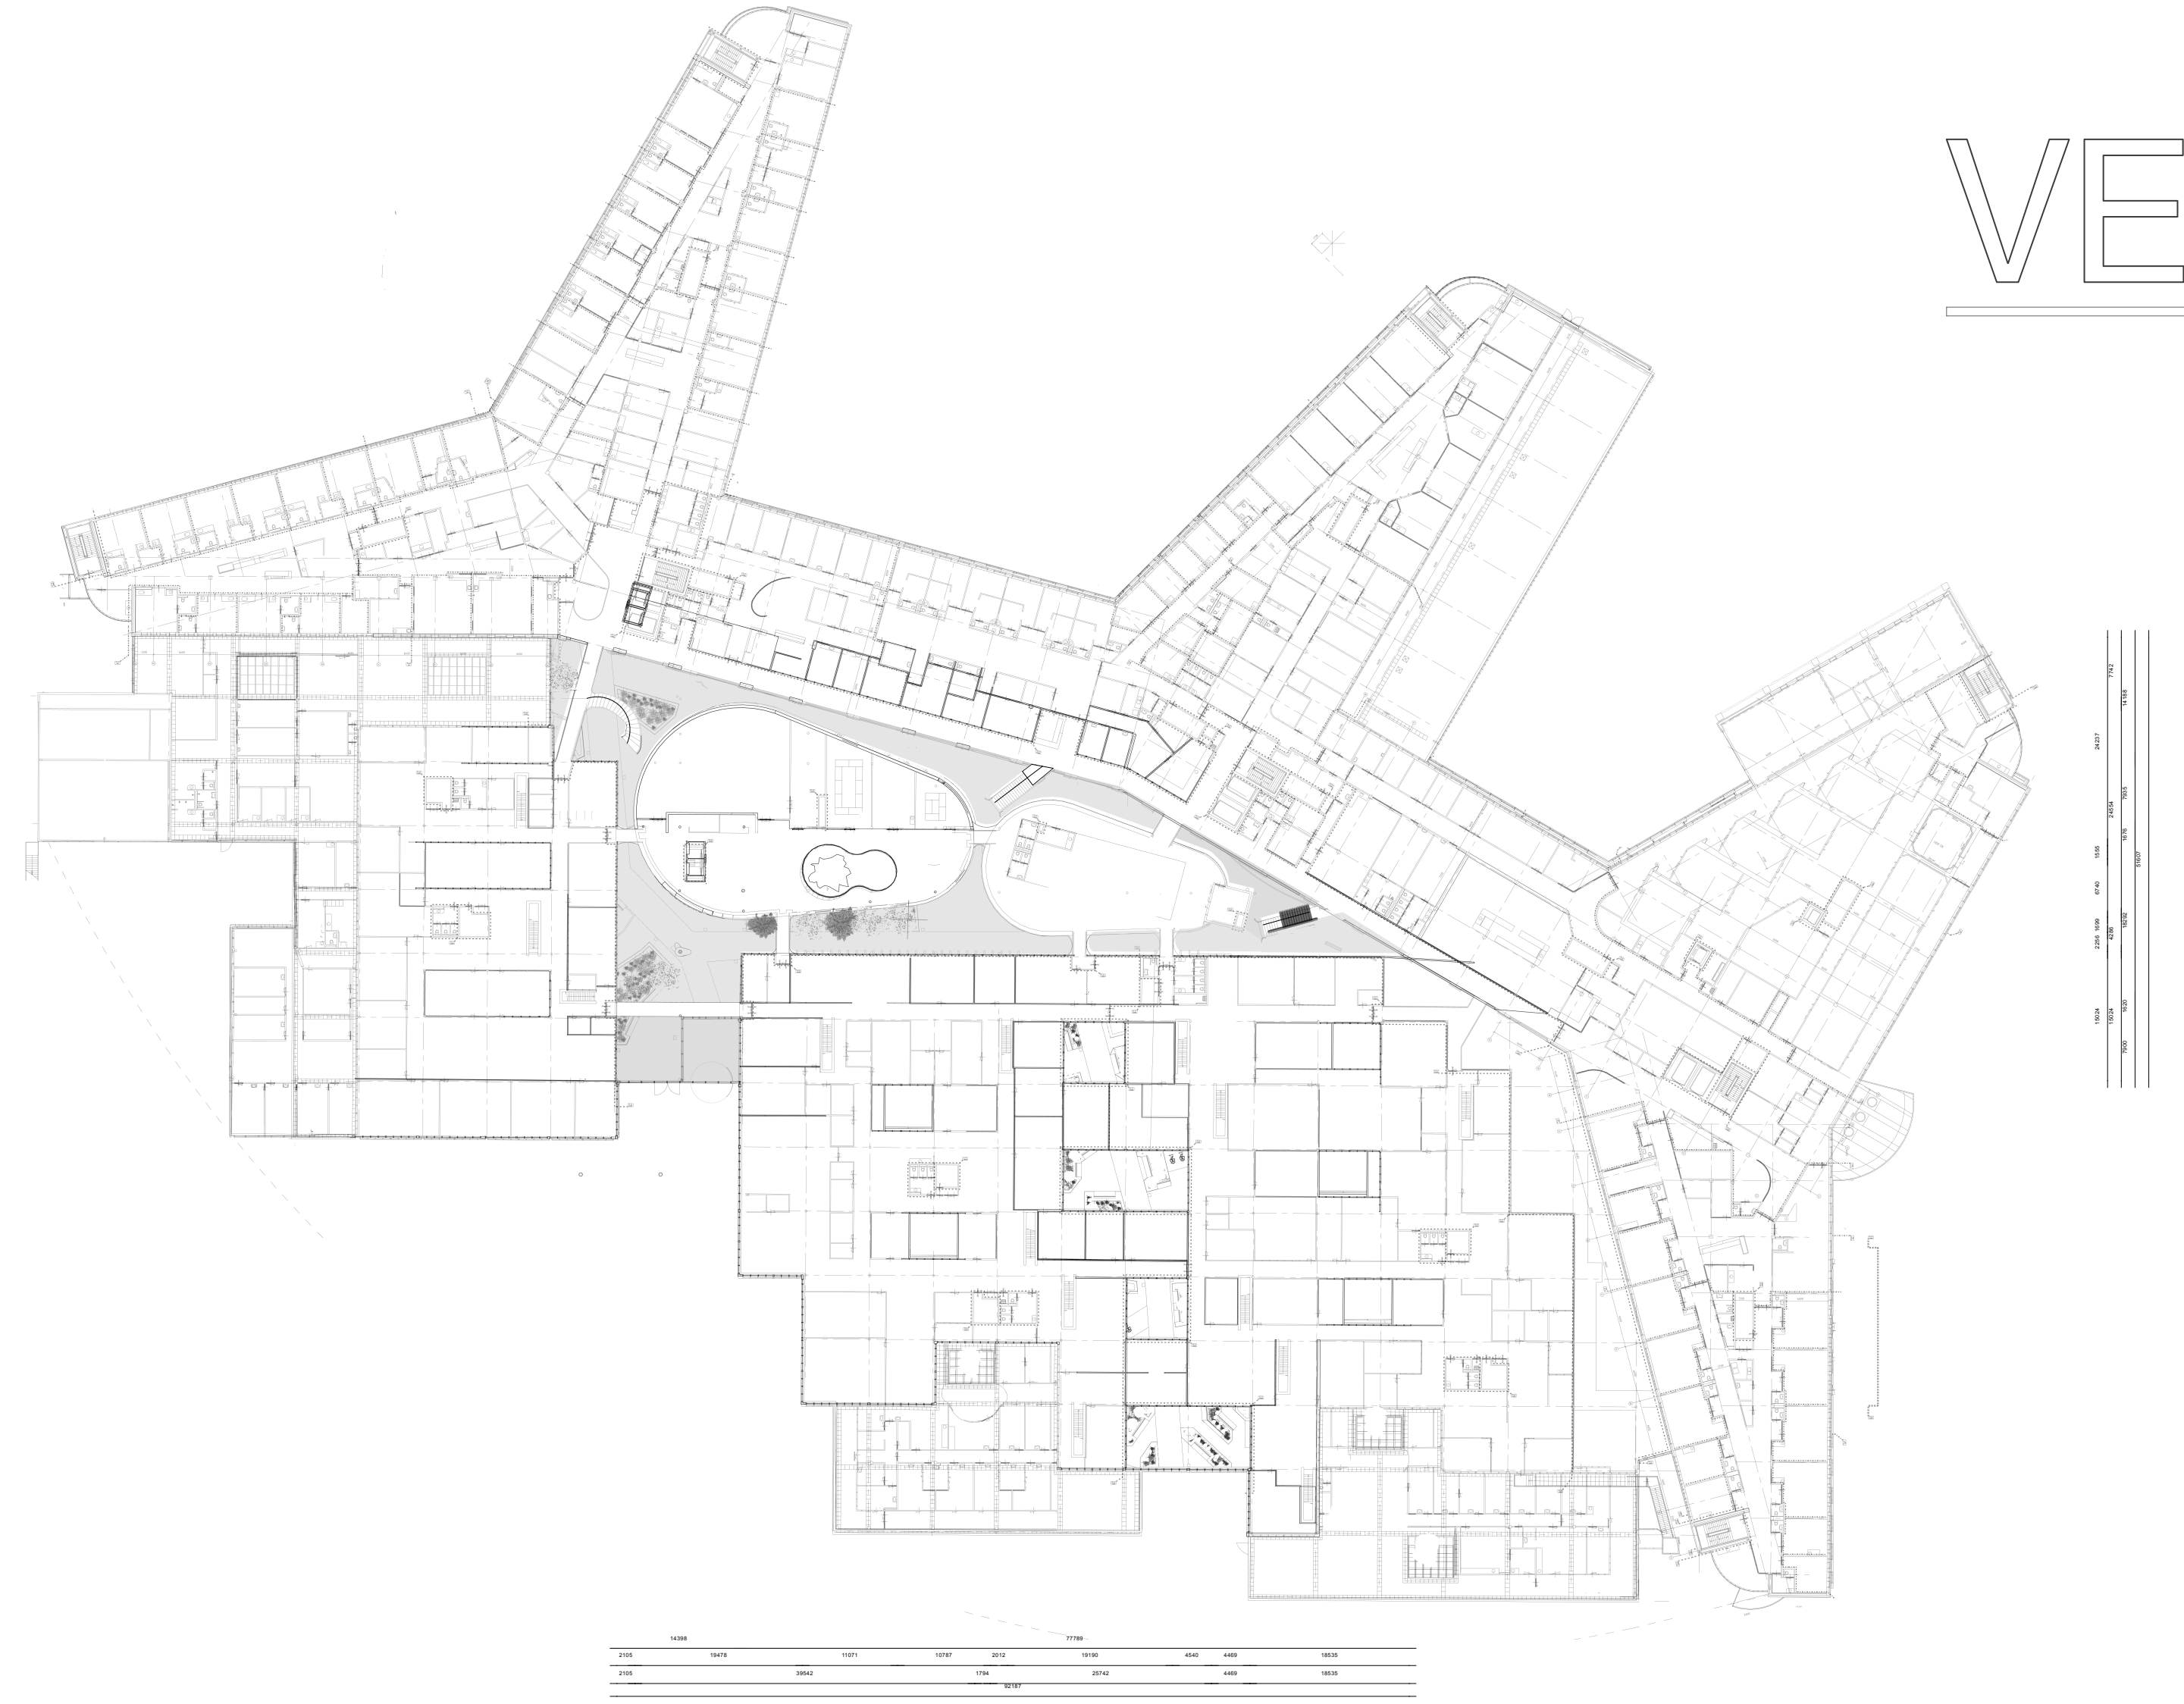

2 Volledige Plattegrond VD
Schaal: 1:500

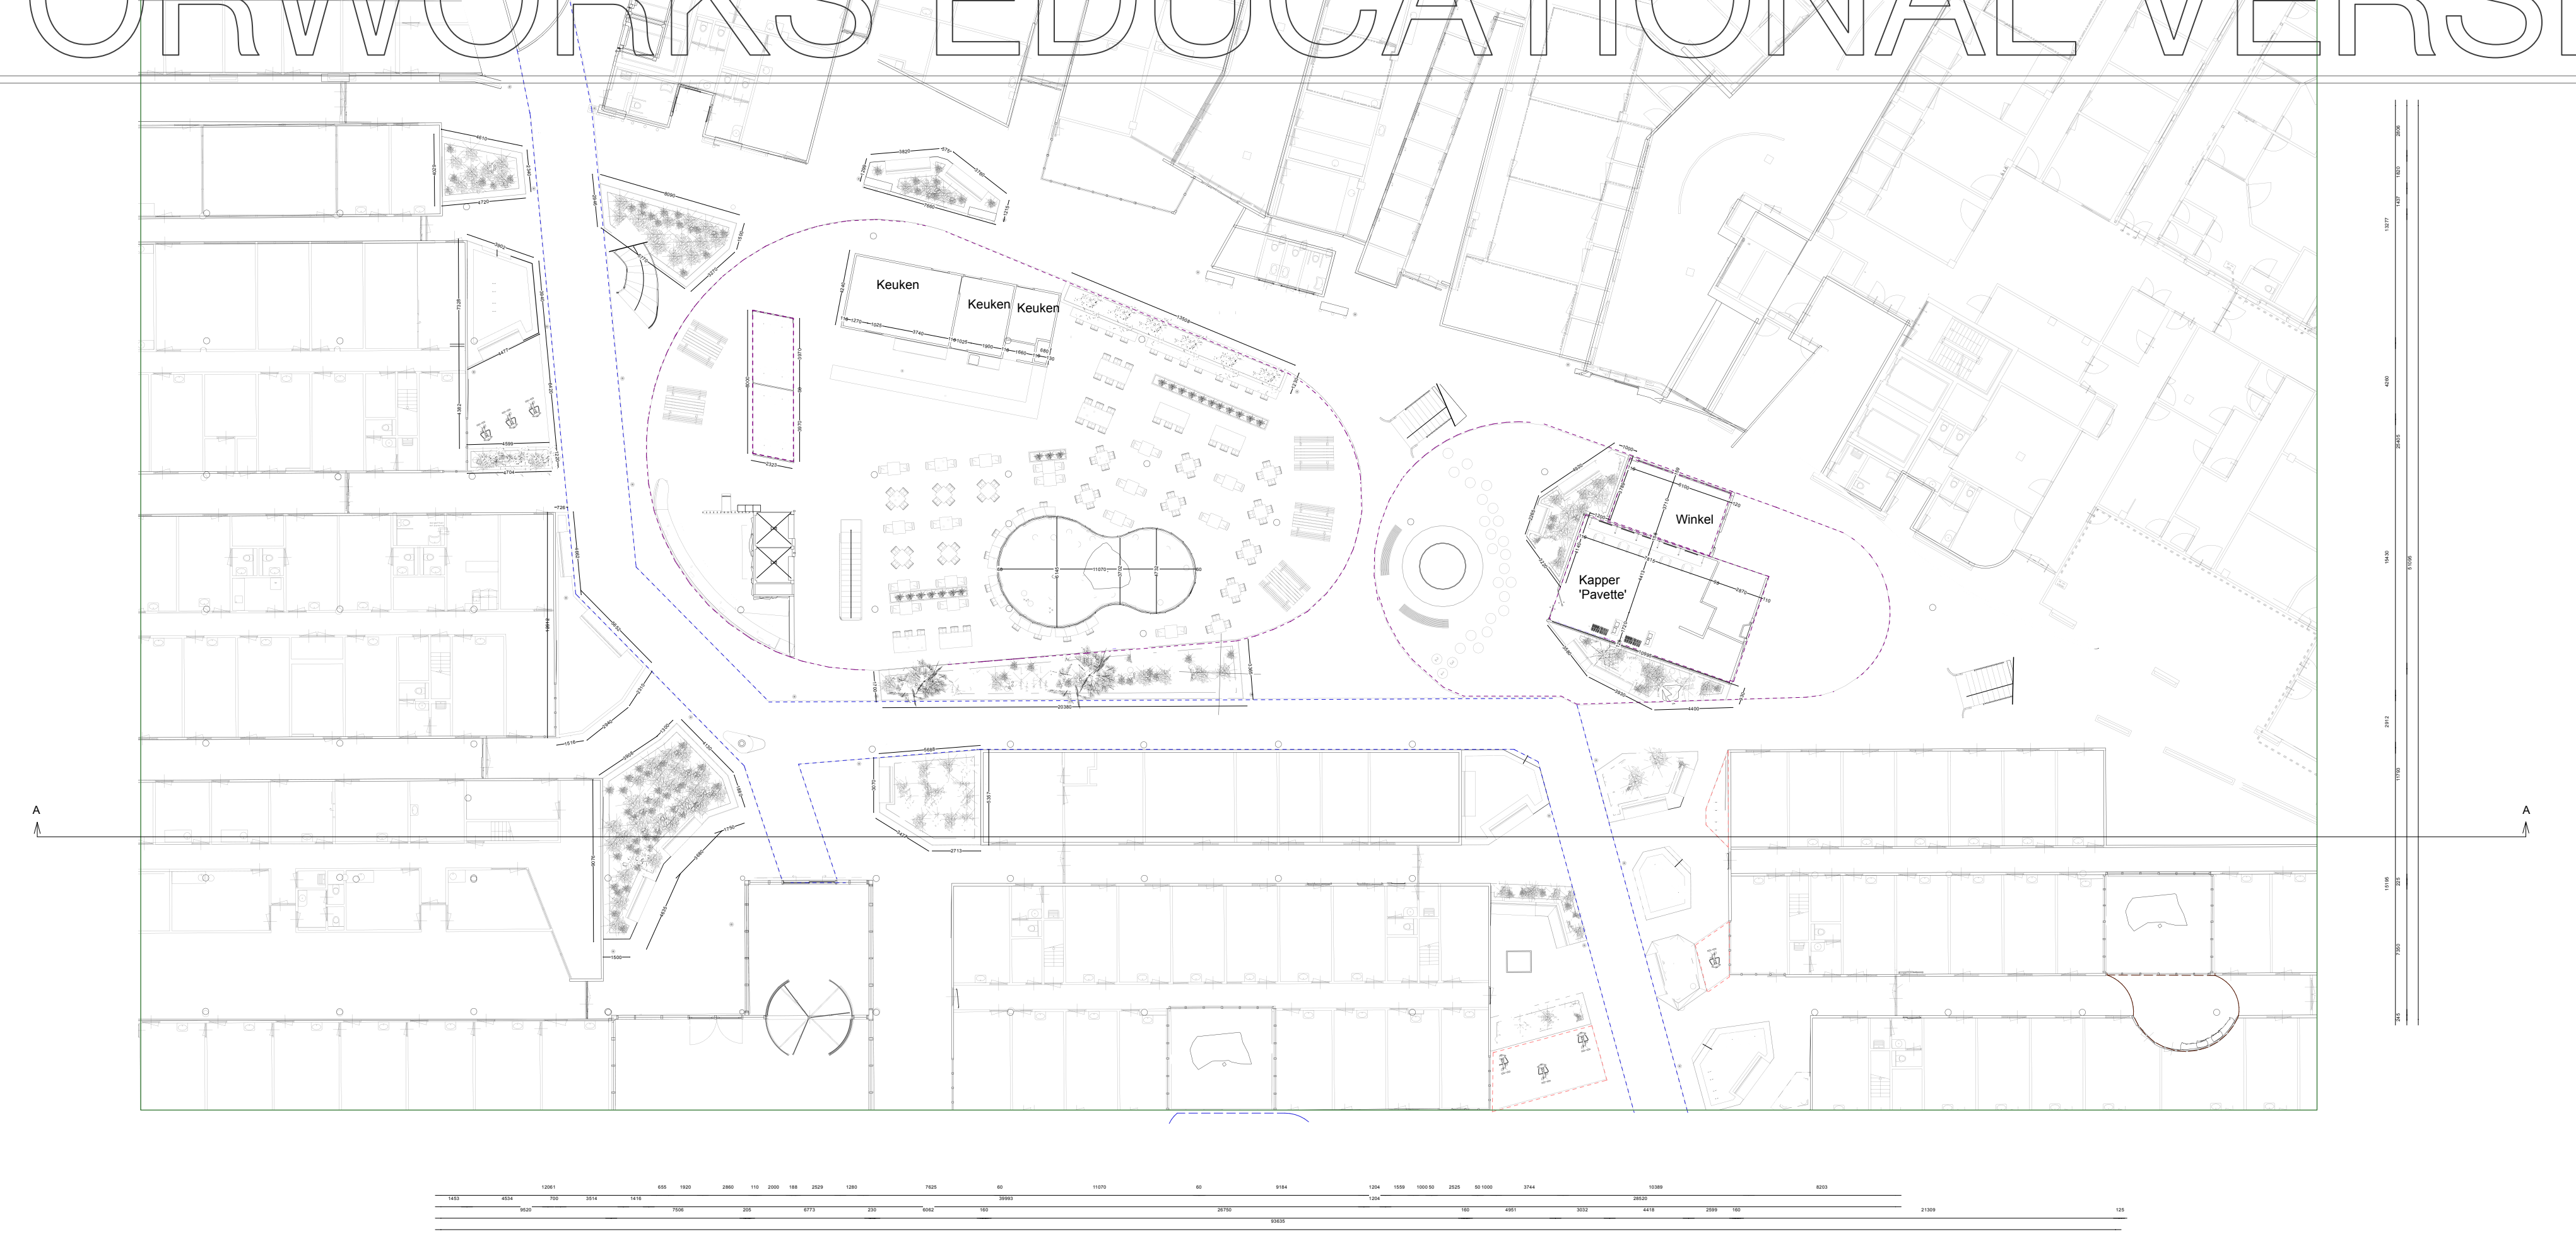

3 Deelplattegrond Centrale Hal
Schaal: 1:200

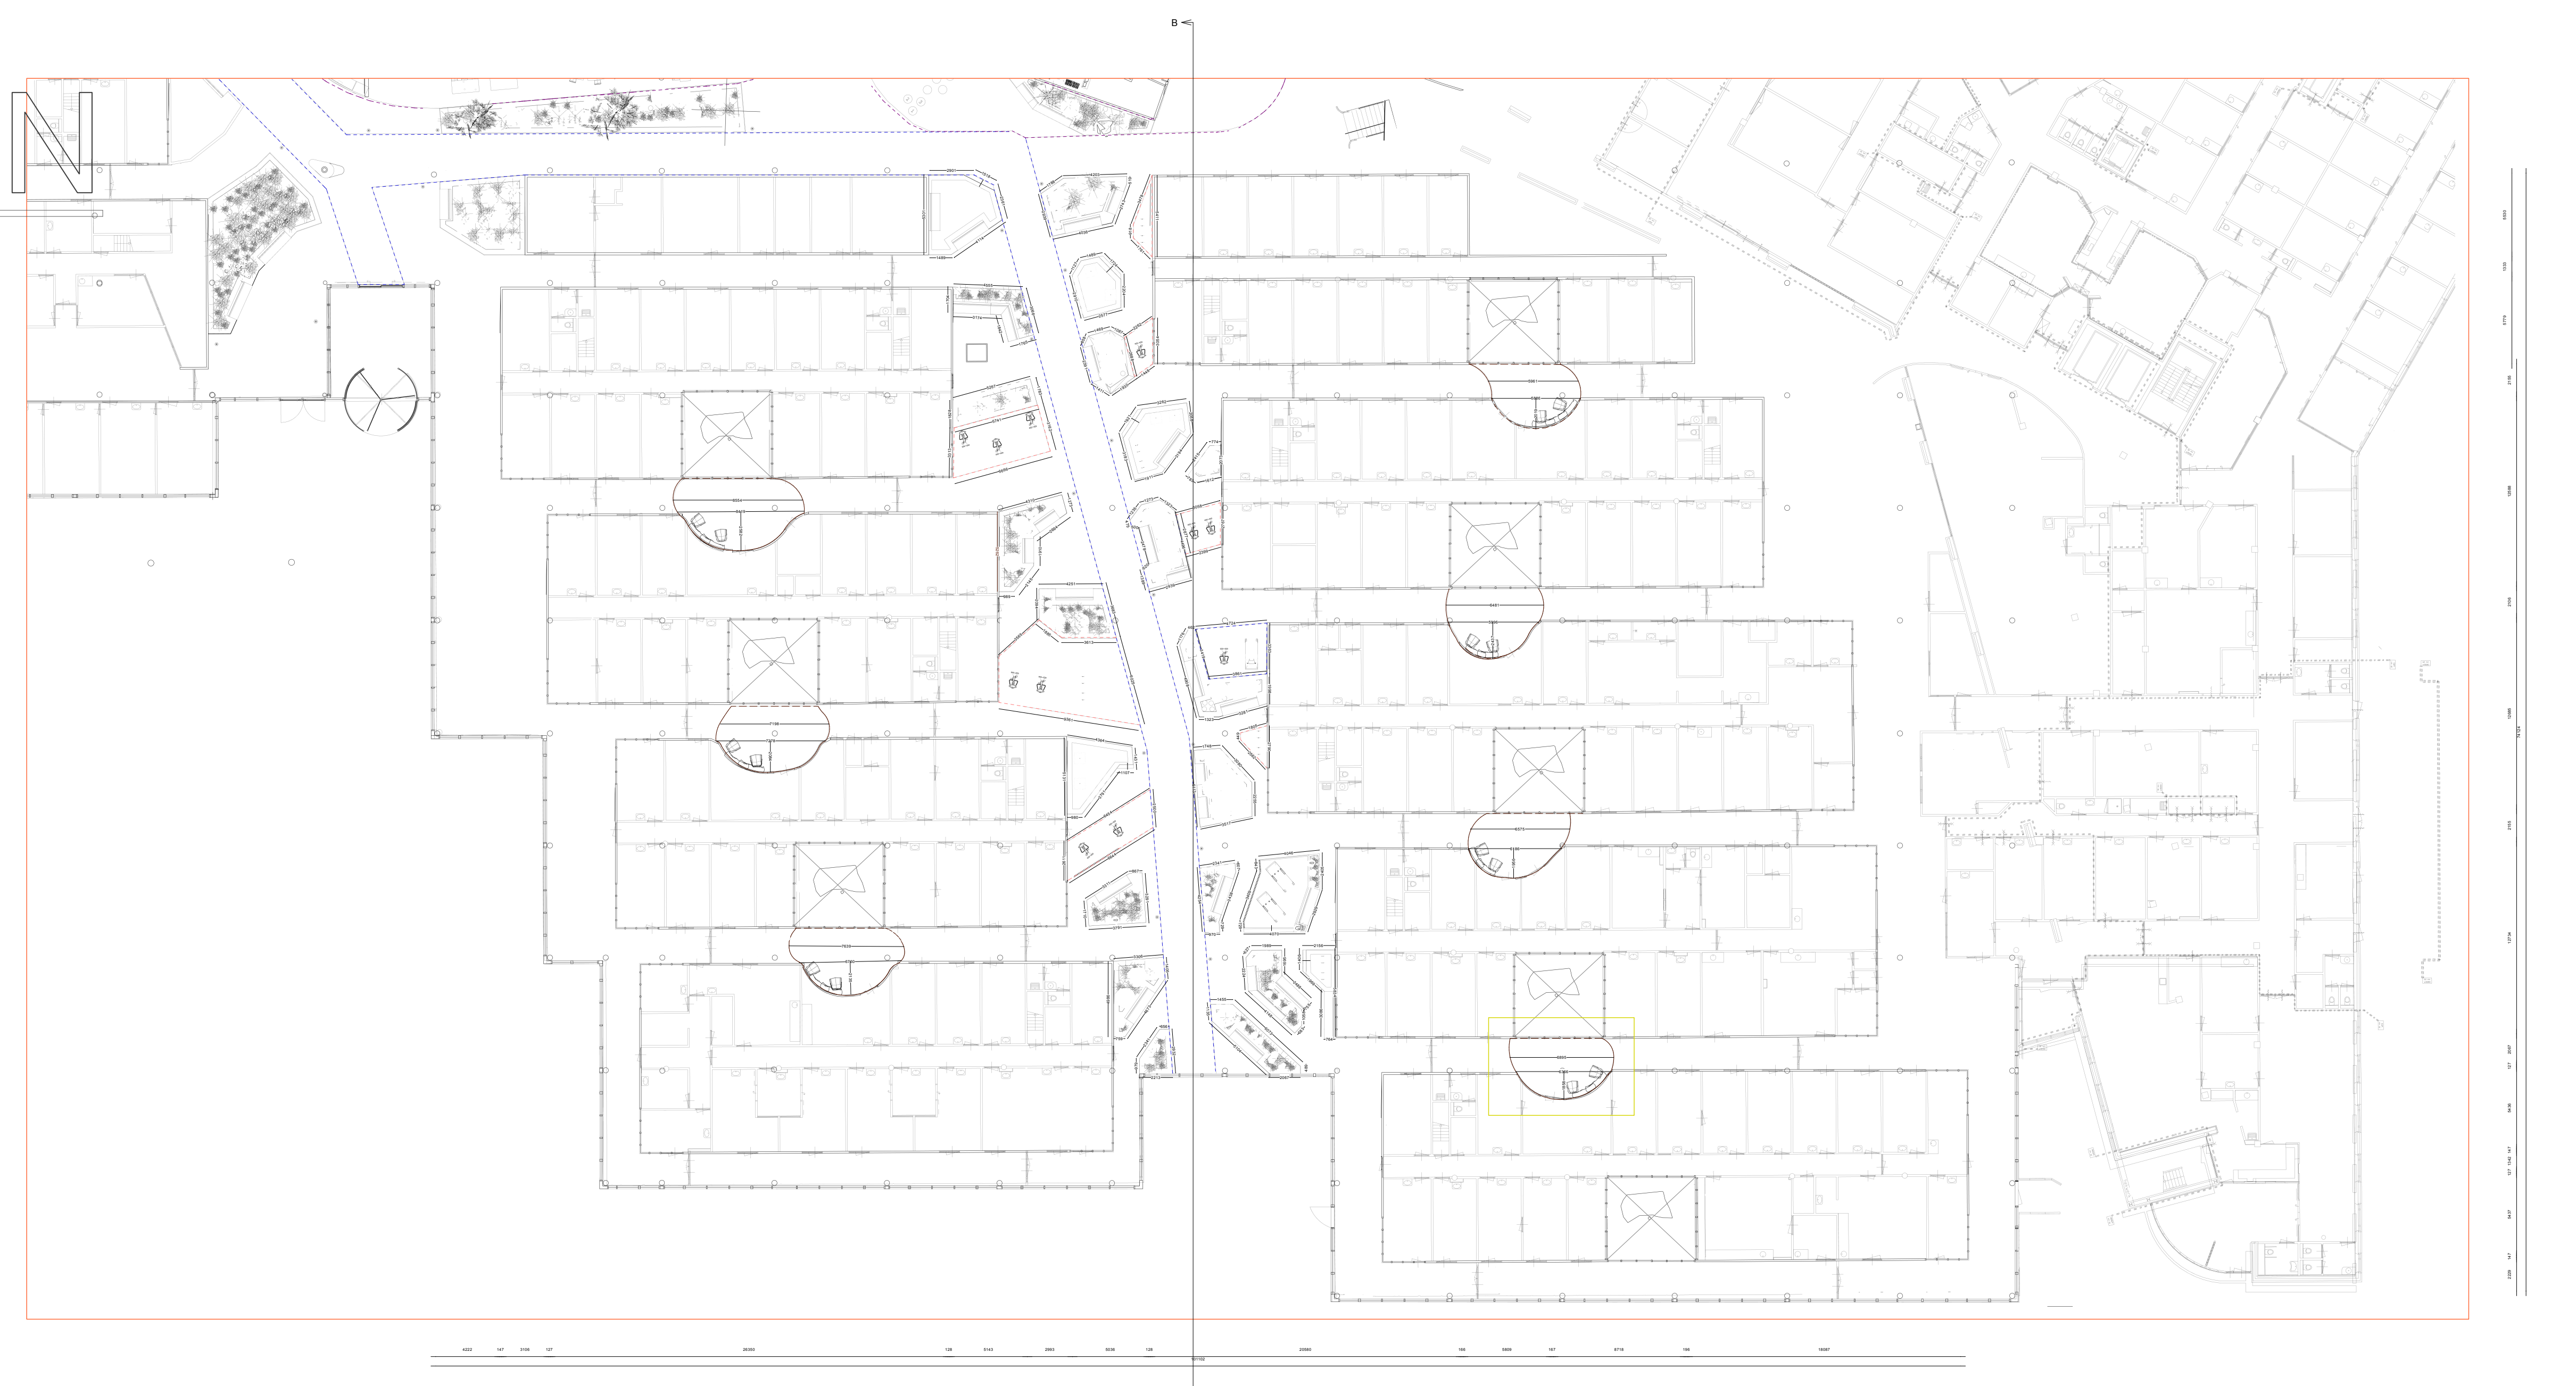

4 Deelplattegrond Poliplein
Schaal: 1:200

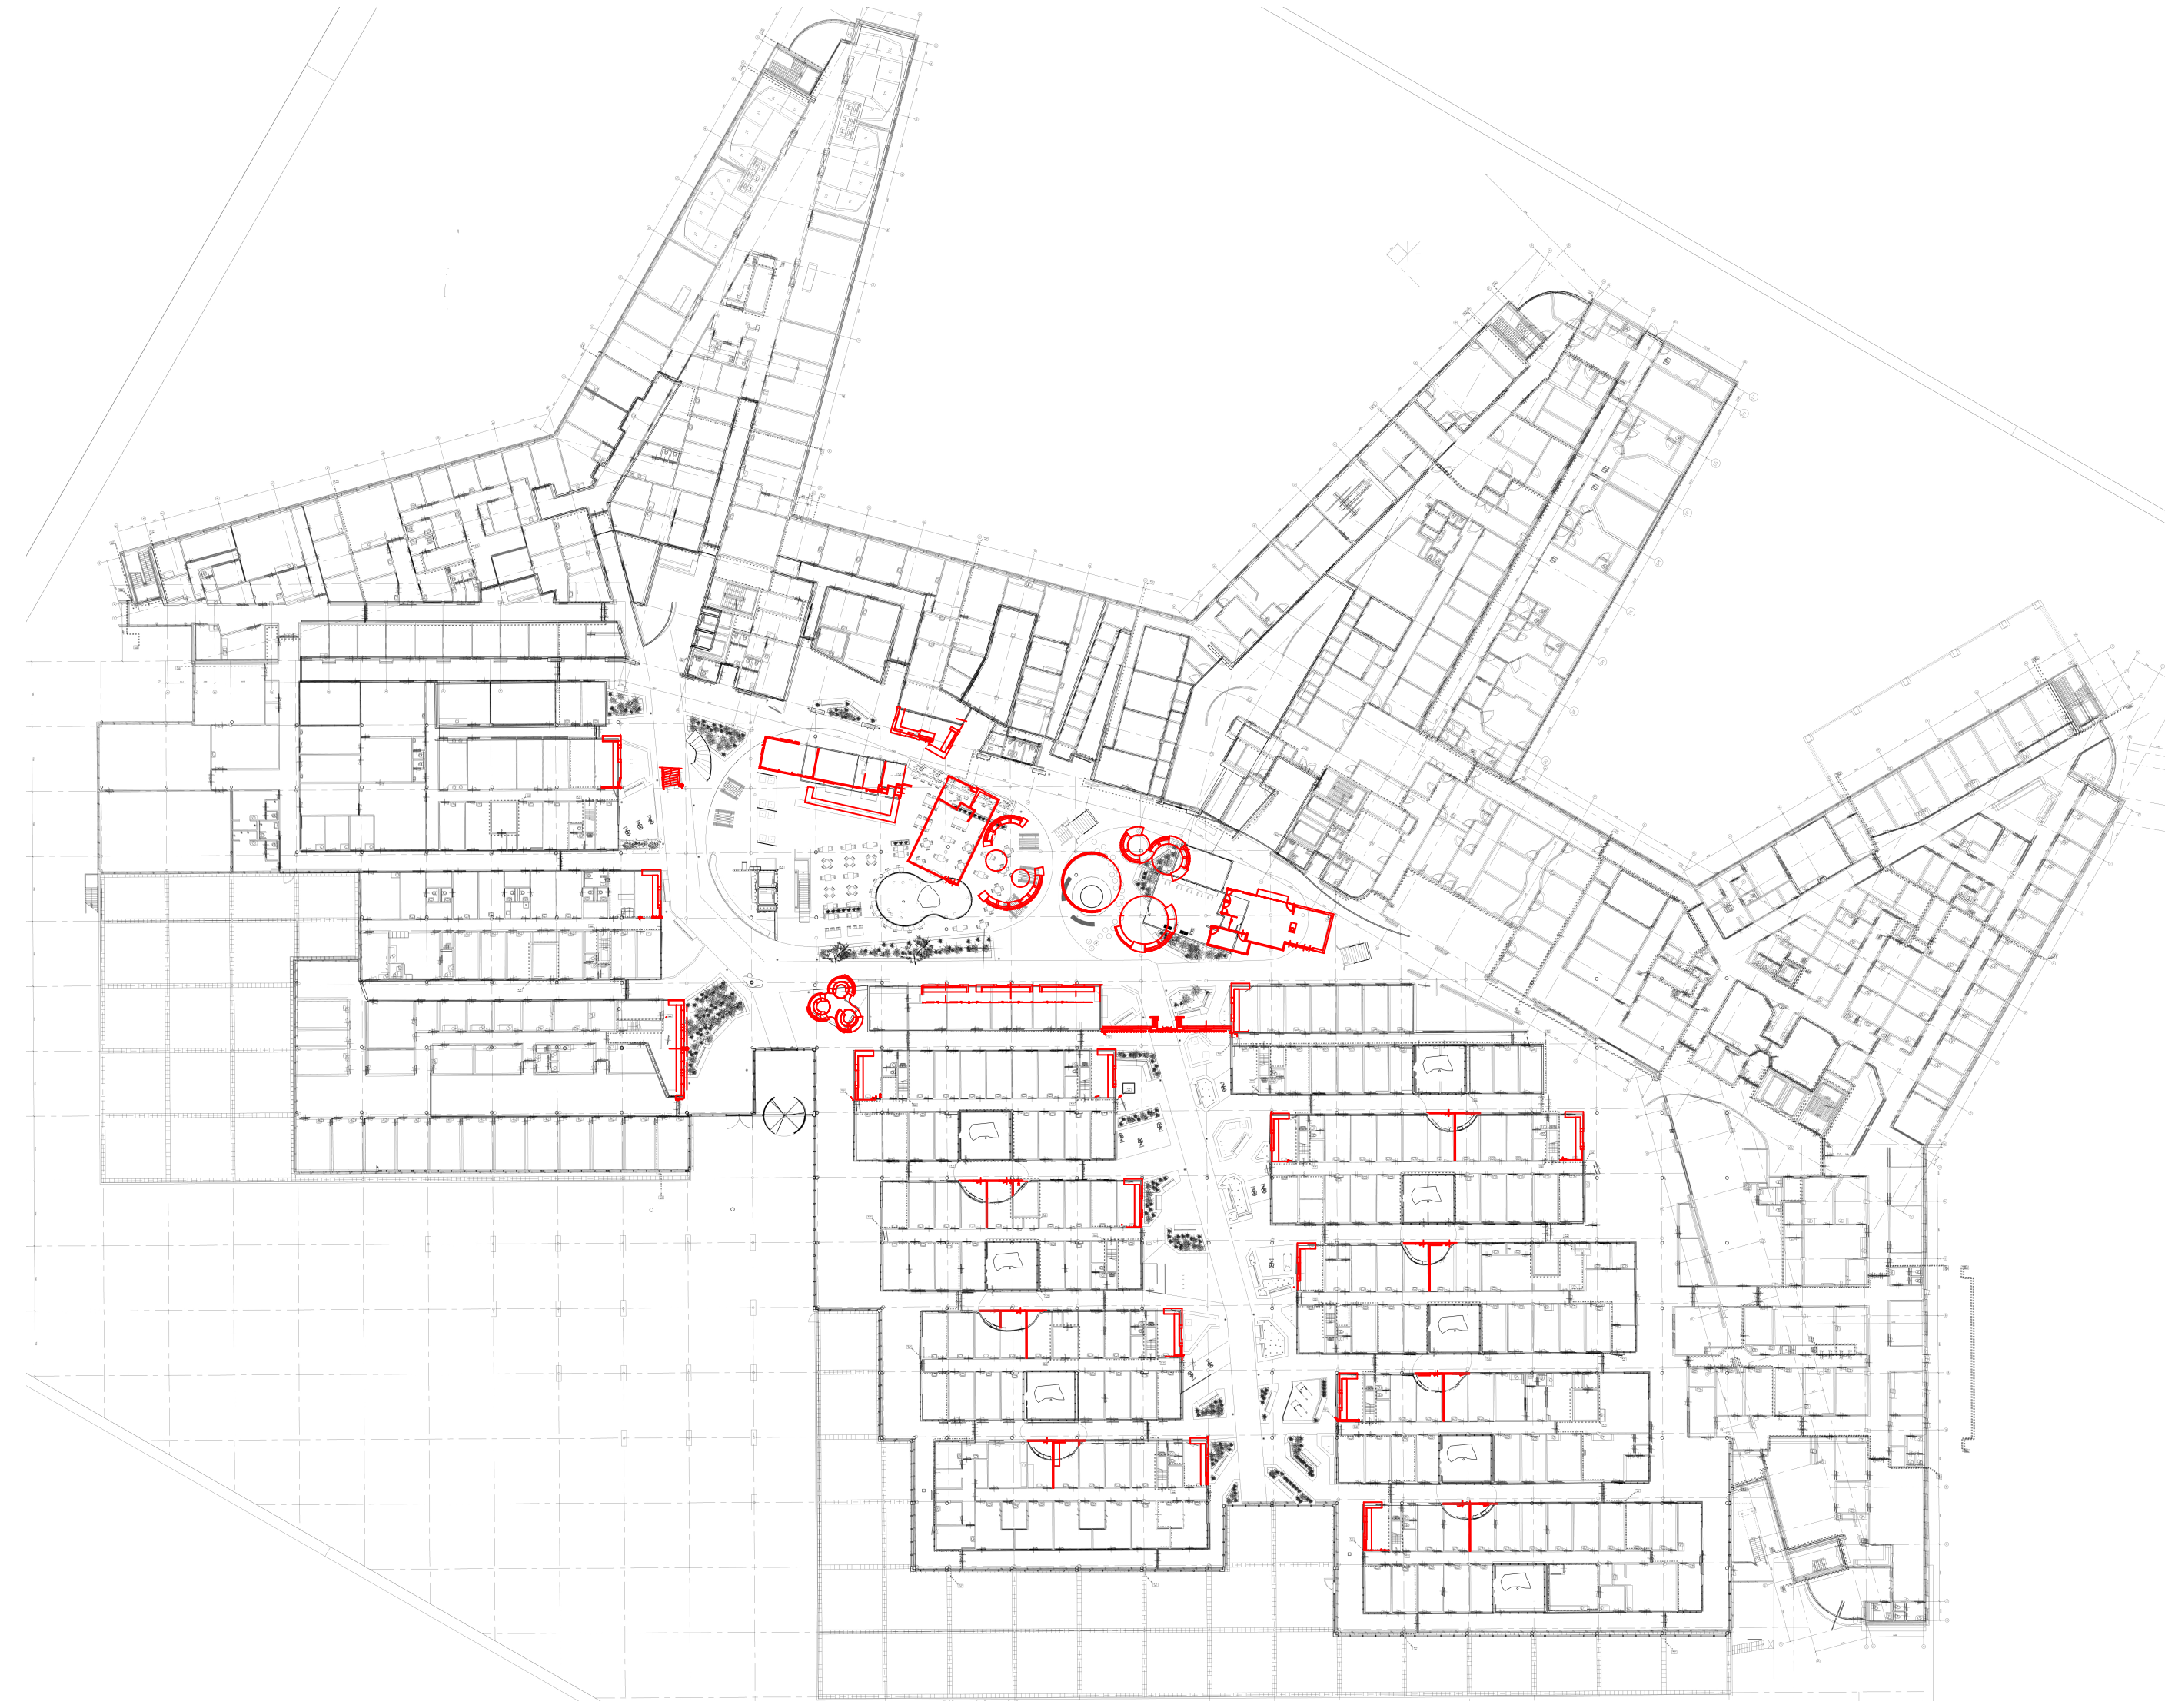

5 Slooptekening
Schaal: 1:500

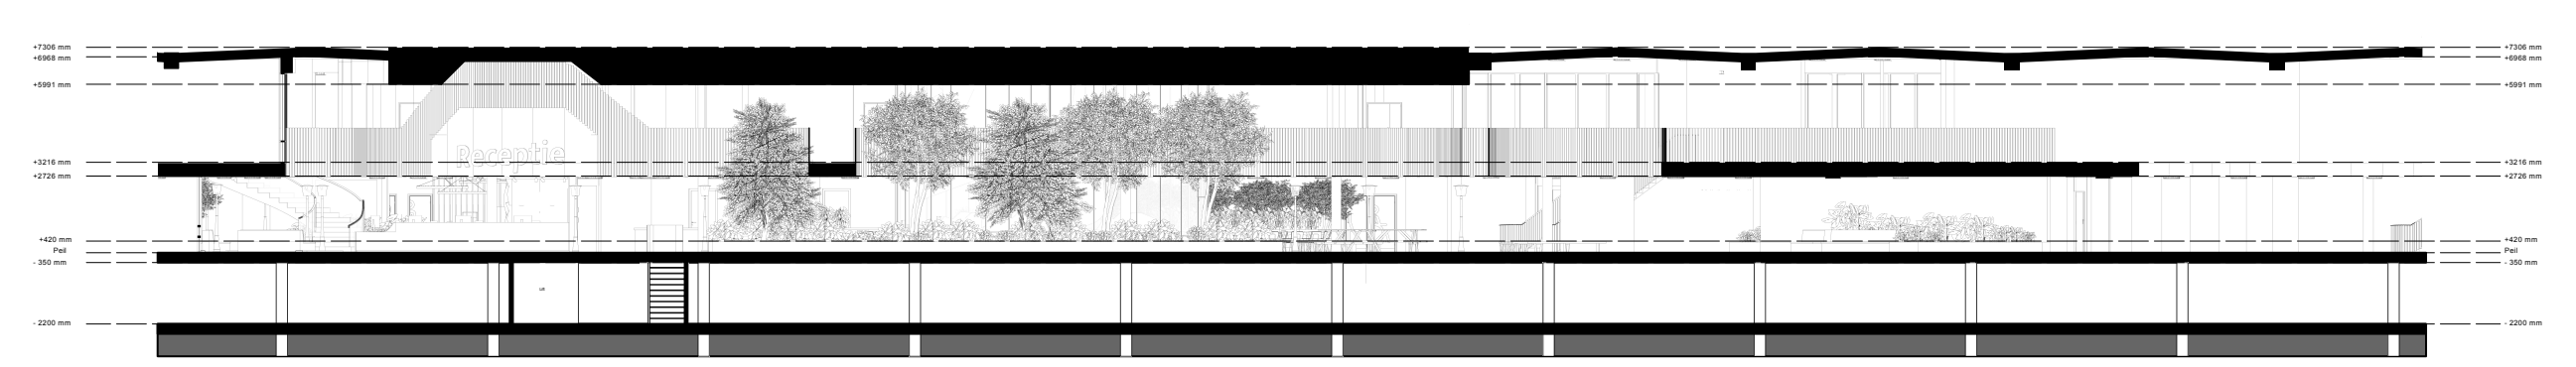

7 Lengtedoorsnede AA
Schaal: 1:200

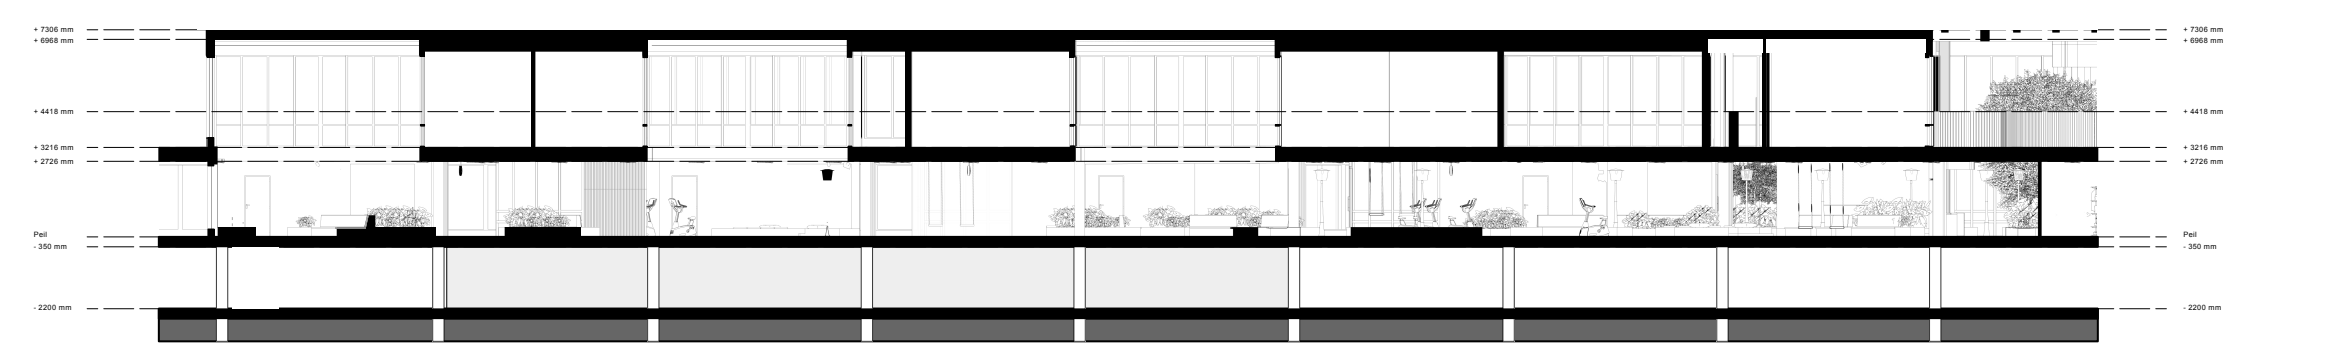

8 Dwarsdoorsnede BB
Schaal: 1:200

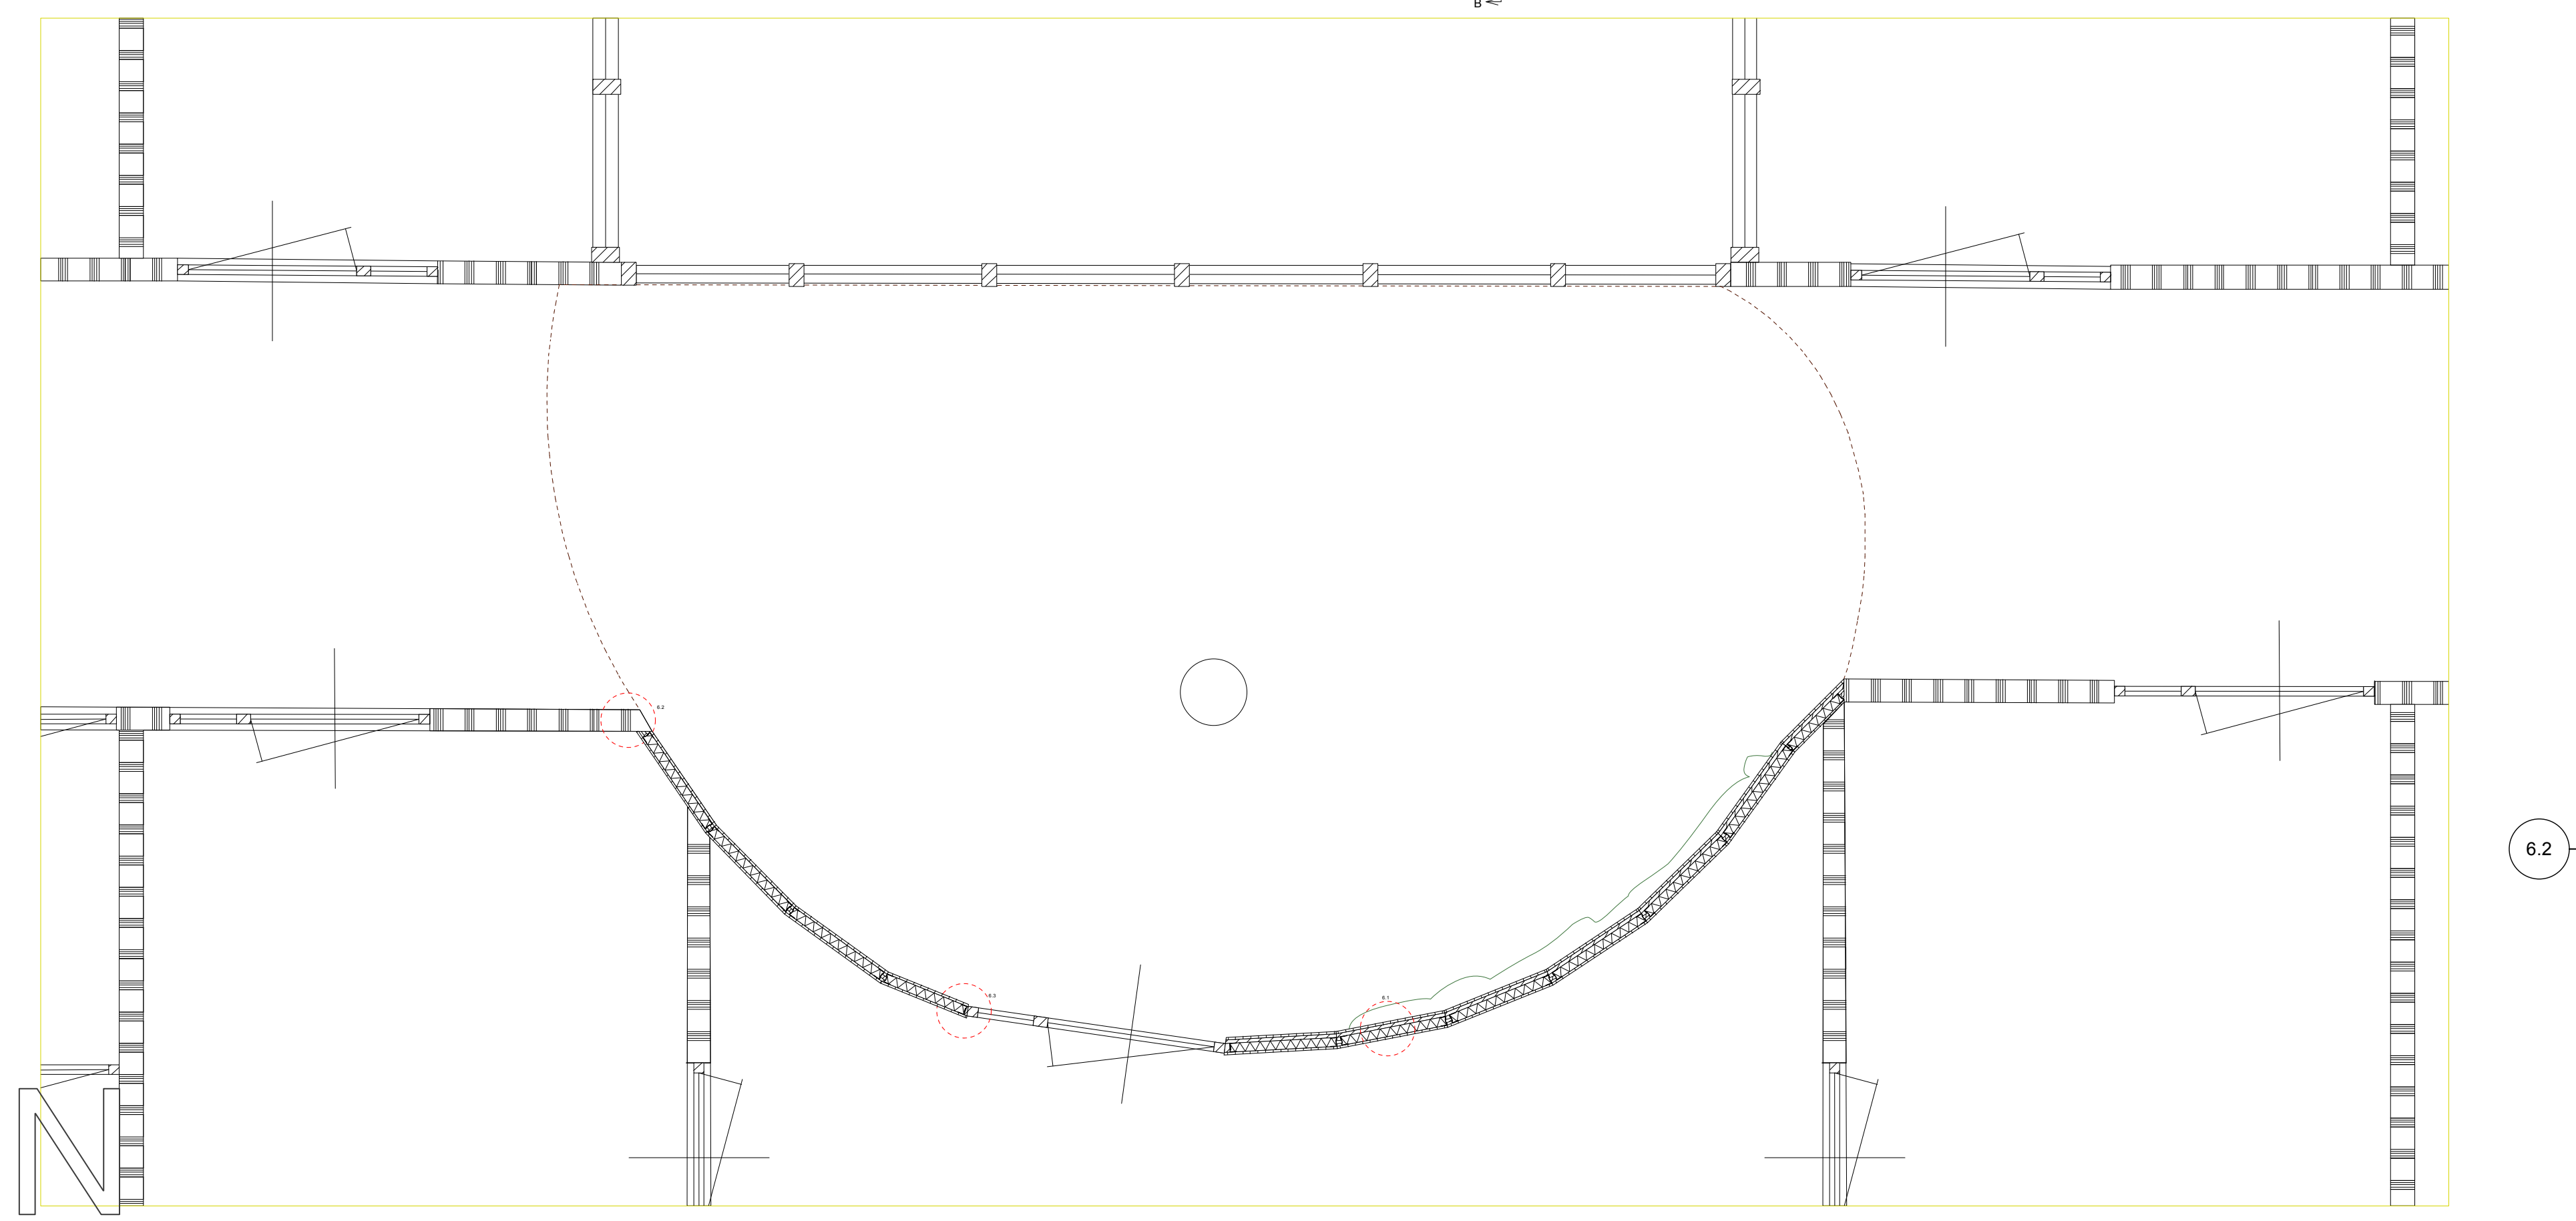

6 Uitsnijding Nest
Schaal: 1:20

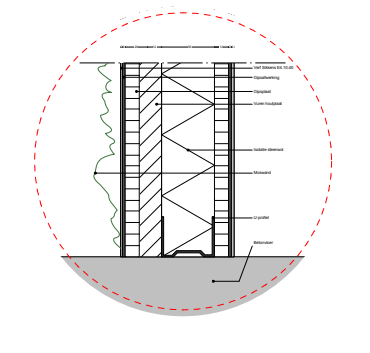

6.1 Detail Lengtedoorsnede wand
Schaal: 1:5

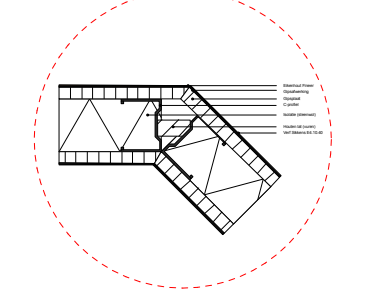

6.2 Detail Dwarsdoorsnede Niet-haakse hoekaansluiting
Schaal: 1:5

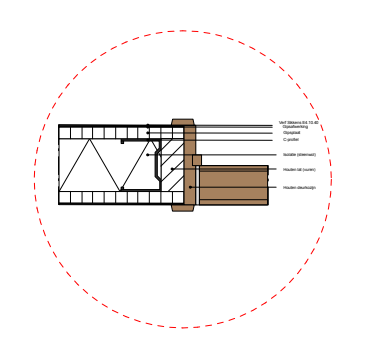

6.3 Detail Deuraansluiting Hout
Schaal: 1:5

Vloerplan Bamboe Supreme Ecru (De Bamboe Hut)
Vloerplan Tegels Mosa Global Collection 75080V
Vloerplan Gerookt Eiken Parket
Vloerplan Tapijt Forbo Tessera Diffusion pivotal moment 2004
Deelplattegrond centrale hal
Deelplattegrond poliplein
Deelplattegrond Nest

Ontwerp: Afstudeeropdracht Deventer Ziekenhuis - Bestektekening
Ontwerper: Guusje Rozendom
Opdrachtgever: Interior Design & Styling
Schaal: 1:5, 1:20, 1:200, 1:500
Formaat: A0+
Eenheid: mm
Datum: 18.01.2024
Tekening nr. 1

VECTORWORKS EDUCATIONAL VERSION