

Minimal Design

Definitief ontwerp

Minimal Design

Kleinere woon-omgevingen met biobaased en milieuvriendelijke ontwerpprincipes

Projectnaam: Minimal Design appartement
Datum: 07/03/2023
Opdrachtgever: Minimal Design Eco

Ontwerper: Guusje Rozendom STUDIO8
E-mail: 499805@student.saxion.nl

Dit ontwerp is het intellectueel eigendom van STUDIO8, zonder toestemming van STUDIO8 is het niet toegestaan dit ontwerp te gebruiken.

De getoonde afbeeldingen zijn sfeerbeelden en mogen niet als werktekening worden beschouwd. Kleuren, maten en structuren kunnen afwijken, graag bekijken wij deze met u samen aan de hand van echte kleurmonsters.

Inhoud

04	Debriefing
06	Onderzoek en pve
08	Plattegrond en ruimte impressie huidige situatie
10	Nieuwe situatie plattegrond
11	Materialisatie
12	Impressies dag-opstelling
14	Impressies flexibele opstelling
18	Lichtplan
20	Impressies lichtplan
22	Maatwerk Ori Living Cloudbed
23	Maatwerk wandkast
24	Maatwerk verschuifbare kast
25	Detail onderstel verschuifbare kast Ori Living
26	Doorsnede verschuifbare kast
27	Detail bureau verschuifbare kast
28	Detail bureau verschuifbare kast

DEBRIEFING

OPDRACHTGEVER: Minimal Design Eco
Bedrijfsnaam: Minimal Design Eco
Voor achternaam contactpersoon: Kasper Spoorman
Datum aanvraag: 21-02-2023

ONTWERPVRAAG:

Ontwerp een appartement met duurzame woonoplossingen gebaseerd op ecologische en milieuvriendelijke uitgangspunten. De woning dient geschikt te zijn voor starters op de woningmarkt, young professionals die de kwaliteit van een goed ontwerp kiezen boven de kwantiteit van een grote ruimte.
Werk met ruimtebesparend meubilair. Flexibele en meervoudig indeelbare plattegronden en slimme keuzes op het gebied van design, esthetiek, installaties, verlichting en materiaalgebruik. Minimalistische vormgeving is noodzakelijk in kleinere ruimten. Geen, of zo min mogelijk, visuele ruis. Heldere, functionele ontwerpen zonder overbodige details bieden overzicht en rust.

ONDERZOEKSVRAAG:
Hoe kan ik een functioneel ontwerp maken in een zo klein mogelijke ruimte, zonder de kwaliteit van de ruimte te beperken.

ACHTERGROND:
Minimal Design is een design startup. Een ontwerpbureau dat zich richt op kleine(re) appartementen en woonomgevingen. Ze ontwikkelen duurzame woonoplossingen gebaseerd op ecologische en milieuvriendelijke uitgangspunten. De woningen zijn geschikt voor starters op de woningmarkt, young professionals die de kwaliteit van een goed ontwerp kiezen boven kwantiteit van een grote ruimte. Maar ook voor anderen die inzien dat een op maat gemaakt ontwerp altijd aantrekkelijker is dan confectie.

DOELGROEP:
Young professionals (starters op de woonmarkt)

AANLEIDING:
Minimal Design zoeken naar ontwerpen die zij kunnen aantonen als voorbeeld van hun bedrijf.

OPLEVERING: Juli 2023

RANDVOORWAARDEN:

- Multifunctioneel, ruimtebesparend meubilair
- Duurzame woonoplossingen
- Flexibele, meervoudig indeelbare plattegronden
- Ten minste een klein appartement (28 tot 35 m2)
- Natuurlijk licht en het beperken van indrukken
- Maak gebruik van biobased materiaal, als niet mogelijk - circulaire materialen

- Kleur-/materiaalgebruik: Minimaal

Uitkomst 1e gesprek:

Denk mee in hoe Minimal Design eruit zou kunnen zien. Je mag kleuren gebruiken, maar maak hier bewuste keuzes in. Zoek zelf een appartement, bijvoorbeeld op Funda. Maak hiervan een long- en short-list. Het hoeft niet goedkoop, maar wel relevant voor de doelgroep. Elk team ontwerpt 4 appartementen, minimaal een kleine (28 tot 35m2) en een middelgrote (40 tot 55m2).
Wij (als studio) zijn de ontwerpers van hun bedrijf. Onze naam wordt vermeldt als het project wordt gepubliceerd.

Huidige situatie:

Niet bestaand vanuit opdrachtgever
Zelf een appartement zoeken

Budget:

Geen budget, houd wel rekening met de doelgroep.

Wie zijn young professionals?

Met de groep young professionals bedoelen we meestal de **starters** op het woon- en werkveld. Deze mensen zijn tussen de **21 en 35 jaar** oud, recent **afgestudeerd** aan hbo of de universiteit en nu aan het werk ofwel in een bedrijf of als **zzp'er**. Het stereotype van deze groep is een obsessie te hebben met **succes behalen**. (Wikipedia contributors, 2023) Enkele eigenschappen die deze groep beschikt zijn **zelf-expressief, liberaal, ambitieus, ruimdenkend** en **zelfverzekerd.** (AllesoverHR.nl, 2018) Ze zijn op zoek naar **zinvol werk, een flexibele omgeving** en **sterke relaties.** (Mørch, z.d.) Om een beter beeld te geven van deze doelgroep, heb ik een persona gecreëerd. Deze is hiernaast te zien:

Sanne en Laura



Wat kenmerkt Sanne en Laura als persoon?

- *Creatief*
- *Optimistisch*
- *Ruimdenkend*
- *Zelfverzekerd*
- *Sociaal*

Wat doen Sanne en Laura?

- *Hebben een baan als grafisch ontwerper*
- *Drinken graag een kopje koffie op een terras*
- *Gaan graag naar musea*
- *Zijn geïnteresseerd in zelfverbetering*

Sanne en Laura

24 en 26 jaar oud

Sanne en Laura zijn beide grafisch ontwerpers. Ze zijn net afgestudeerd en werken nu bij Oase Creative en Optimalprint.

Ze wonen samen en hebben een kat, Oscar. In hun vrije tijd houden ze zich graag bezig met films kijken op Netflix en lezen.

Wat Sanne en Laura's behoeftes?

- *Rust thuis*
- *Work-life balance*
- *Willen verbondenheid met hun omgeving*

Wat zijn Sanne en Laura's interieur voorkeuren?

Ze willen graag centraal in een stad wonen. Ze hebben belang voor duurzaamheid en willen dit ook in hun interieur. Sanne en Laura willen een betaalbare woning met veel opbergruimte, grote ramen en goede isolatie.

PERSONA

MINIMAL DESIGN

Foto door Ivan Samkov: https://www.pexels.com/nl-nl/foto/creatief-werken-werkruimte-opstarten-5428637/

Onderzoek naar pijnpunten en wensen wat betreft interieur bij young professionals

Wens en sfeer

Uit onderzoek naar de woontrends van young professionals (Hales, 2011) zijn een aantal aandachtspunten gebleken, waar wij rekening mee kunnen houden bij het ontwerpen. Bronnen suggereren dat young professionals vaker in **centrale steden** gaan wonen. Deze groep zal op zoek gaan naar **betaalbare woningen**, in stedelijke gemeenschappen die goed verbonden zijn via het **openbaar vervoer** (JRC, 2009).

In hetzelfde wetenschappelijke artikel heeft Hales (2011) onderzoek gedaan naar 'Ontwerpen voor Young Professionals'. Dit onderzoek suggereert dat de volgende problemen spelen in de leefomgeving van young professionals:


- Structurele/ontwerpgebreken
- Te weinig opbergruimte
- Te kleine slaapkamers
- Te warm/te koud
- Te luidruchtig
- Geen privacy
- Te ver van het centrum/werk/sociaal leven etc.

Farnsworth (2001) identificeert daarentegen de belangrijkste woonvoorzieningen van deze groep:


- Extra aanrechtruimte in keuken
- Overvloedige opbergruimte en kasten
- Energiezuinig
- Grote ramen
- Buiten leefruimte
- Flexibel indeelbare ruimte
- Hoge plafonds
- Duurzaam
- Een thuiskantoor




CENTRAAL
BETAALBAAR
DUURZAAM

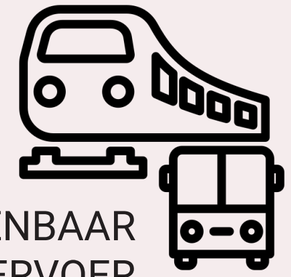

OPENBAAR
VERVOER

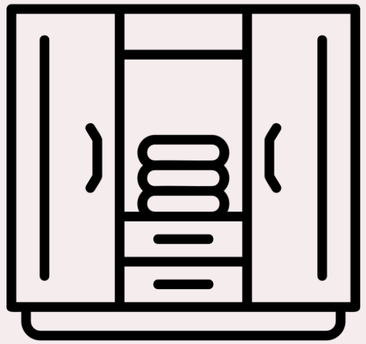

OPBERGRUIMTE

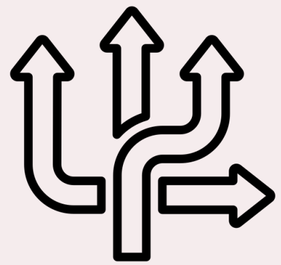


FLEXIBEL
INDEELBARE
RUIMTE



THUISKANTOOR

Plattegrond & ruimte impressie huidige situatie

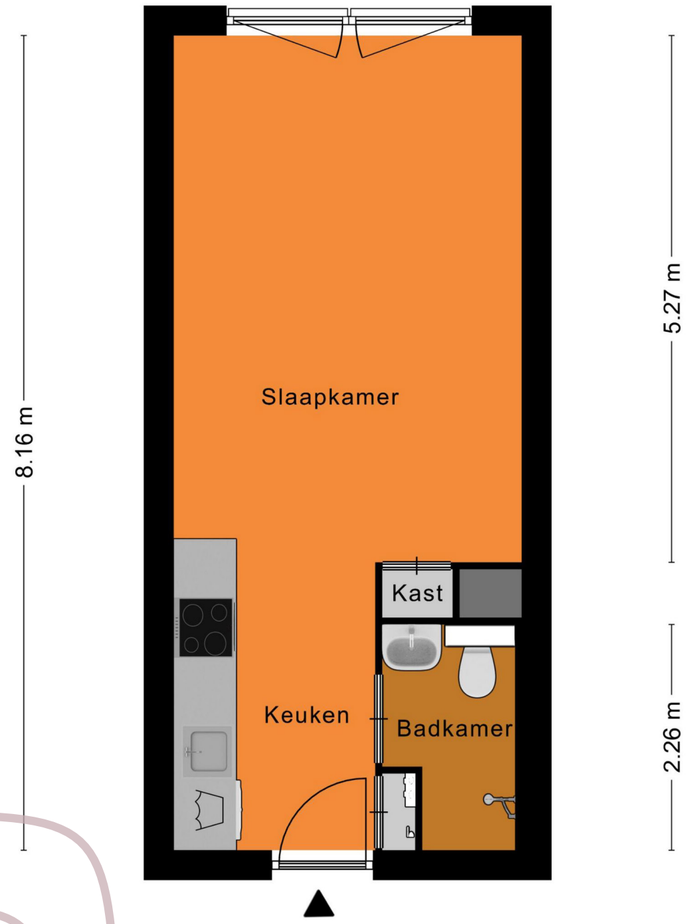









Welnastraat 231, Amsterdam






Voor dit project heb ik een appartement van 28m2 gekozen, gelegen aan de Welnastraat in Amsterdam.
Dit is het kleinste appartement mogelijk voor dit project, ik heb deze gekozen omdat ik mijzelf wou uitdagen. Met de onderzoeksvraag **'Hoe kan ik een functioneel ontwerp maken in een zo klein mogelijke ruimte, zonder de kwaliteit van de ruimte te beperken.'** ging ik aan de slag.
Ik onderzocht de behoeften en pijnpunten van de doelgroep young professionals (zie p. 07).
Uit dit onderzoek bleek dat young professionals graag in een bruisende stad wonen, met voldoende mogelijkheden om alles makkelijk te kunnen bezoeken, eventueel met bereikbaar openbaar vervoer. Daarnaast is duurzaamheid in het appartement ook erg belangrijk. (zie voor verder onderzoek naar deze doelgroep pagina 06).

Op basis van deze voorwaarden ben ik opzoek gegaan naar appartementen in de hoofdstad, Amsterdam. Dit appartement aan de Welnastraat 231 in de wijk Amstelkwartier Noord, ligt op bereikbare afstand van het bruisende centrum van Amsterdam. Rondom het appartementencomplex zijn voldoende parkeerplekken en een supermarkt, restaurant en andere winkels liggen op de begane-grond onder de appartementen.

Dit appartement is gebouwd in 2011 en heeft energielabel A. Het is volledig geïsoleerd met dakisolatie, dubbelglas, muurisolatie en vloerisolatie. Het heeft internet via glasvezel.

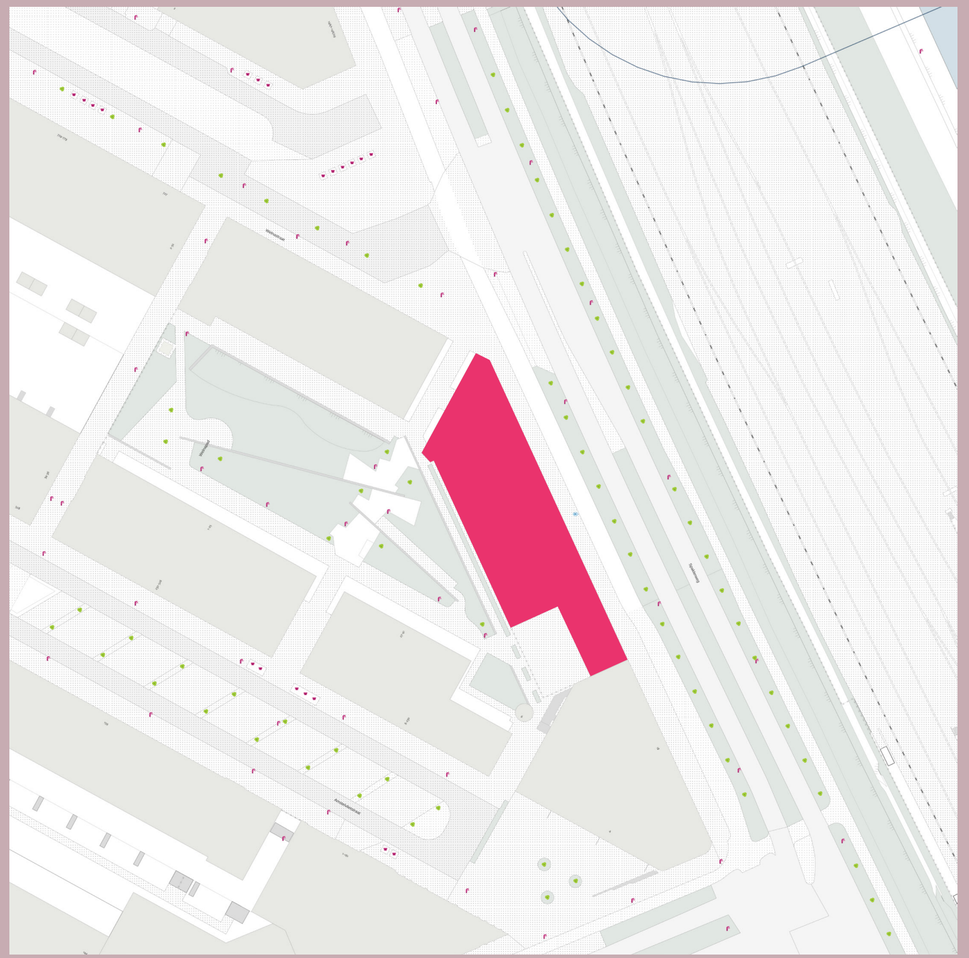


Nieuwe situatie

Het appartementencomplex is een bestaand gebouw, daardoor hebben de keuken, badkamer en meterkast een vaste plek. Dit zorgt voor **18 m2 overgebleven ruimte voor vier verschillende functies**, namelijk wonen, eten, slapen en werken. Daarnaast is het belangrijk dat er voldoende opbergruimte is.
Om dit te behalen, maak ik gebruik **multifunctioneel, flexibel inzetbaar meubilair.**
Op de plattegronden heb ik het ontwerp getoond in een dag- en nacht-opstelling.


Het multifunctioneel, flexibel inzetbaar meubilair is (bijna) allemaal eigen ontworpen **maatwerk**.

Ten eerste zie je bij binnenkomst aan de linkerzijde van het appartement de keuken. Rechts hiernaast bevindt zich de badkamer en meterkast. Verder in het appartement loop je tegen het 'Cloud bed' aan van het merk Ori Living. Deze woon-/slaapkamer is geaccentueerd door middel van een vloerkleed, hierdoor lijkt het een apparte ruimte in het appartement.
Aan de rechter zijde van deze ruimte staat een verschuifbare opberg- en kledingkast en een wandkast, die ook fungeert als tv-meubel, bureau, eettafel en extra zitplekken.

Op de volgende pagina's worden de functies van de multifunctionele maatmeubels verder uitgelicht.

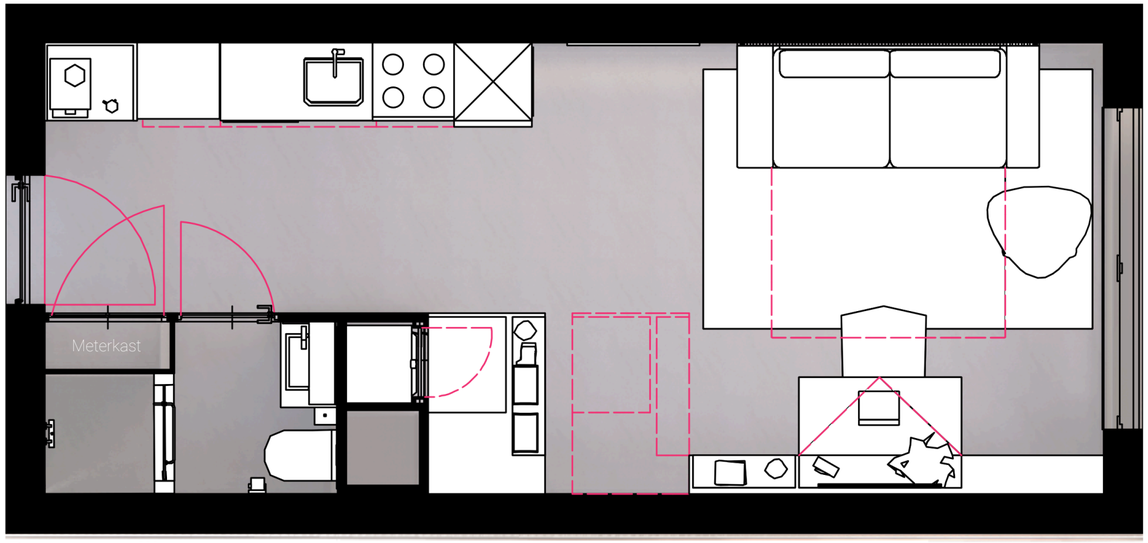

Dag-opstelling

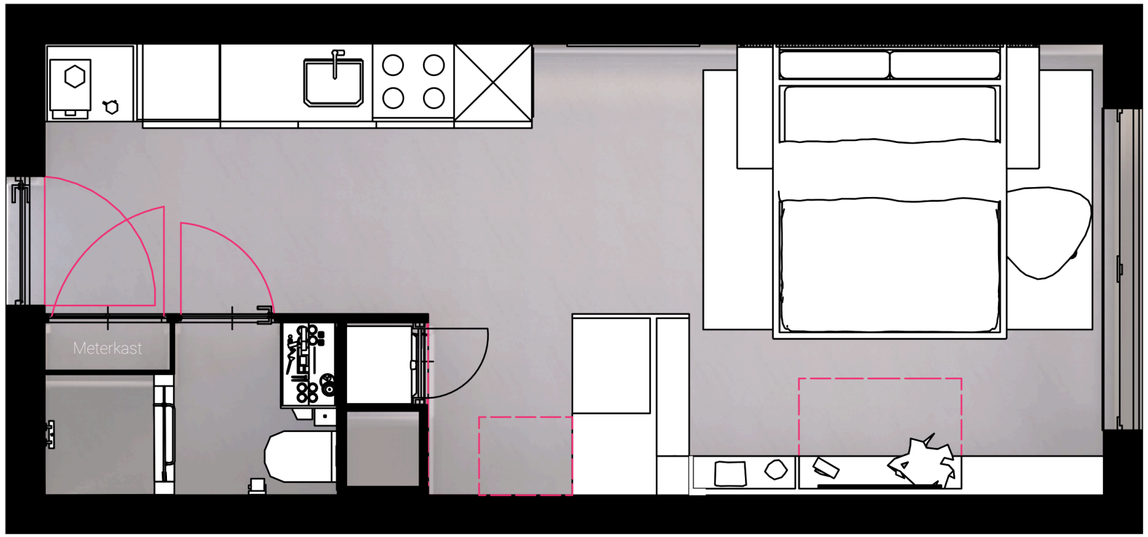


Nacht-opstelling

Materialisatie





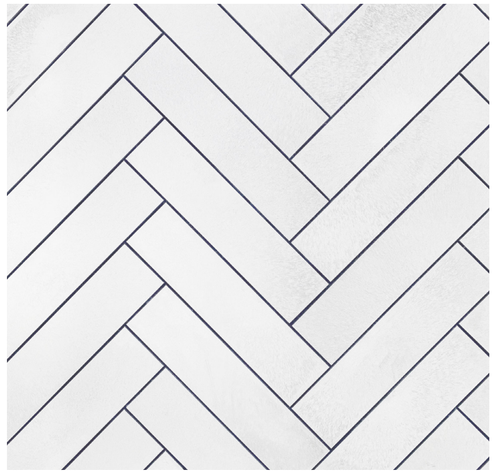





Omdat het appartement zo klein is, is het nodig om **rust** te creëren door **zo min mogelijk visuele ruis** toe te voegen. Dit houdt in dat er geen onnodige details in het appartement zijn. Deze rust laat ik ook terugkeren in het appartement door **aardse kleuren en materialen** te gebruiken. Het kleuren pallet dat te zien is in het appartement bestaat uit groen, gebroken wit en donker blauw. Het materiaal dat te zien is, is eikenhout en een beton-look marmoleum vloer. Voor meer informatie over materiaal en kleur in het appartement, zie het **A5 boekje 'Materiaal'**. In dit boekje ga ik dieper in op de **biobased en duurzame** eigenschappen van ieder individuele materiaal.

De materialen die ik gebruik in dit ontwerp zijn:

Vloer:	Forbo flooring systems, Marmoleum Fresco
Verf:	Fairf, Krokodil en Overtoom
Tegels:	OVpolymers, The Coffee Tiles
Plaatmateriaal:	Pantoni hout, kern Stabilo decor Vicenza eik
Vloerkleed:	Desso, Tarkett Flagstone

Impressie dag-opstelling





Toelichting dag-opstelling

Op de eerste afbeelding kijk je tegen het Cloud bed van het merk Ori living aan. Je zou het bed een upgrade van het murphy bed kunnen noemen. Door middel van een contragewichtsysteem verwerkt in de achterwand van dit meubel, verplaatst dit bed zich van het plafond naar beneden met een druk op de knop..
In mijn ontwerp van dit appartement zit de bovenkant van dit meubel, de plek waar het bed zich bevindt, boven het verlaagde plafond. Op deze manier wordt de ruimte meer een geheel.
Verder zie je een wandkast op de eerste afbeelding. Deze wandkast fungeert als tv-meubel, opbergkast, eettafel, bureau en zitplek.
Deze kast heeft een uitklapbare tafel van 1250 bij 600 mm. Deze kan gebruikt worden als eettafel en bureau. Zie voor de zitplekken in de kast de volgende pagina.
Op de tweede afbeelding is de verschuifbare opberg- en kleding kast te zien. De kast verschuift via een rails aan de wand op de grond 1100 mm van de muur. Zo ontstaat er een inloopkast en komt de deur naar de wasmachine vrij. Uit deze kast is een bureau te klappen, voor een tweede werkplek. Zie voor een beeld van deze werkplek de volgende pagina.

Uitwerkingen van deze (maat)meubels zijn te zien vanaf pagina 22.





Toelichting dag-opstelling

Dit appartement is geschikt voor 2 personen, maar wat als je je vrienden zou willen uitnodigen? Hoe maak je van krap vier zitplekken genoeg voor je vriendengroep?
In de wandkast heb ik hier mogelijkheid voor gemaakt. Aan de linkerkant van de wandkast, op een zithoogte van 400 mm, kunnen de kastdeuren opengeklapt worden, om zo twee extra zitplekken te creëren. Op de twee kussens in dit kastdeel staan 2 vouwbare stoelen die ook extra zitplekken bieden. Een van deze stoelen kan ook ingezet worden als bureau stoel bij de extra werkplek, zoals te zien op de tweede afbeelding.
Door een uitklapbaar bureau toe te voegen aan de verschuifbare kast, creëer ik een afgesloten extra werkplek, zodat de twee bewoners van het appartement ongestoord te werk kunnen gaan. Dit uitklapbare bureau is 700 bij 600 mm. Meer details over deze kast en het bureau zijn te vinden op de maatwerktekeningen vanaf pagina 22.







Toelichting dag-opstelling

Op de eerste twee afbeeldingen van deze pagina's is de badkamer te zien. Over de wasbak heb ik een uitklapbare 'make-up tafel' ontworpen, zodat er extra ruimte gecreëerd kan worden in de badkamer. Deze glazen tafel klapt uit over een steunrails bevestigd aan de wand. Hiervoor wordt de kraan gedraaid en in het meubel geduwd.
Op de derde afbeelding van deze pagina's is de keuken uitgebeeld. Hier is te zien hoe de keuken van binnen is verlicht. Aan de rechterzijde van de keuken staat de kast waarin de verschuifbare wand staat. Deze kan verschoven worden via een rails aan de bovenzijde van de keukenkastjes en via zwenkwieltjes aan de onderkant van de vouwmuur-delen. De keuken kan afgesloten worden tot en met de koelkast, om zo geuren uit de keuken te beperken en visuele ruis weg te nemen.


Lichtplan


Mijn lichtconcept is **‘verstopt licht’**. Door de randvoorwaarde ‘zo min mogelijk visuele ruis’ heb ik ervoor gekozen het licht **geïntegreerd** toe te passen. De lichtbronnen mogen hierom niet zichtbaar zijn. Dit pas ik toe door gebruik te maken van een **verlaagd plafond**. Dit plafond bedekt het volledige appartement, behalve de badkamer en meterkast. Tussen het plafond en de wanden zit een ruimte van 185 mm, hier weerkaatst het licht van de **LED-strips** op het plafond, tegen de wand de ruimte in. Het plafond ligt op een hoogte van 2300 mm (in het appartement met een hoogte van 2600 mm), hierdoor is de bovenkant van het Cloud bed ook niet meer te zien, wat bijdraagt aan de **vermindering van visuele ruis**.

Verder heb ik geïntegreerde LED-strips toegepast in elke kast. Deze **plaatsverlichting** zorgt voor meer sfeer in de ruimte, maar is ook praktisch. Zo heb ik dit ook toegepast onder de hangende keukenkasten, zo is er meer licht tijdens het koken.

Als laatst heb ik LED-strips toegepast in de badkamer achter de spiegel en in de douche, de beschermingsklasse van deze verlichting licht hoger dan bij de andere LED-strips, zodat ze **waterbestendig** zijn.

Meer informatie over de verlichting en armaturen staan in het **armaturen boek**.

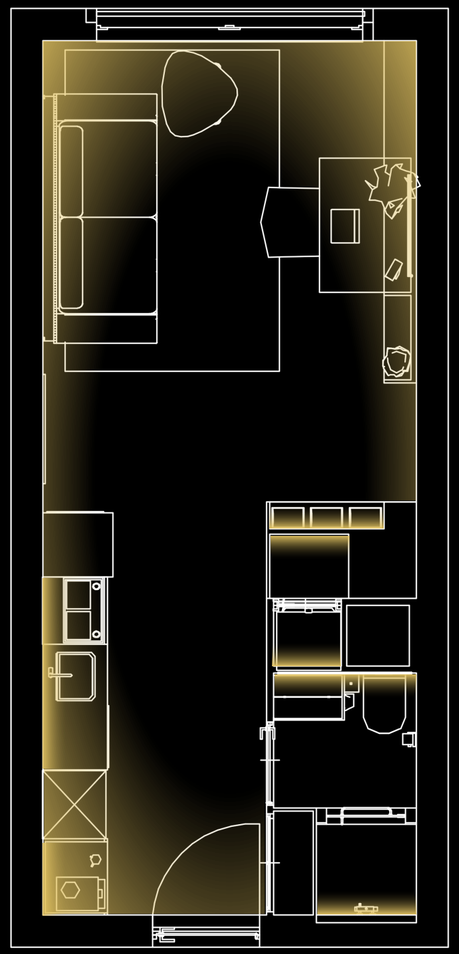


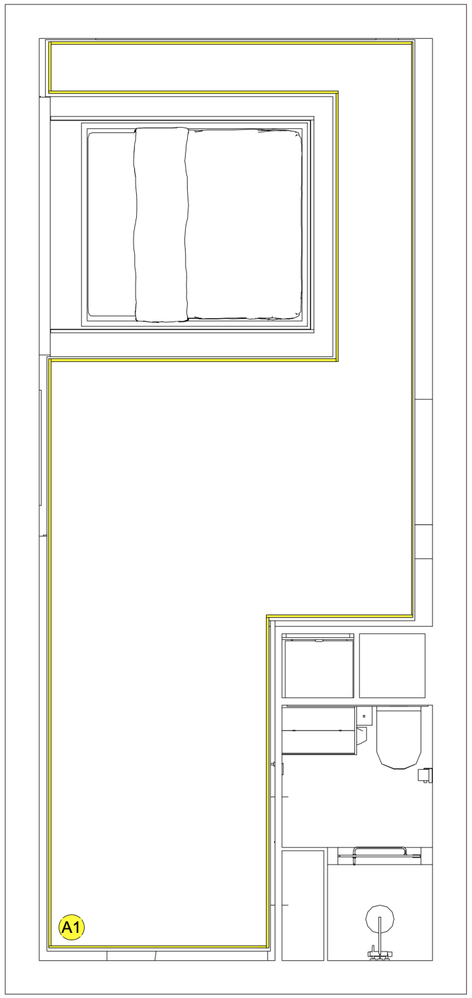


1 Lichtplan verlaagd plafond
Schaal: 1:50



2 Lichtplan onder verlaagd plafond
Schaal: 1:50

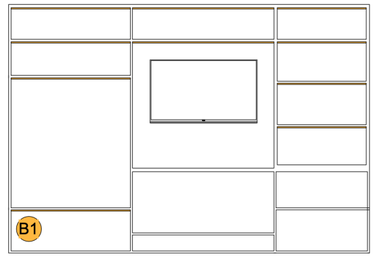


3 Doorsnede wandkast - lichtplan
Schaal: 1:50

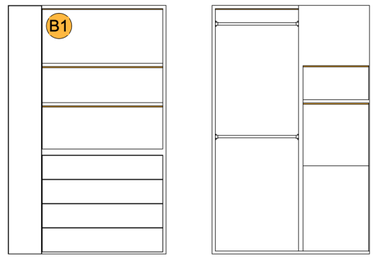


4 Voor- en achteraanzicht verschuifbare kast lichtplan
Schaal: 1:50





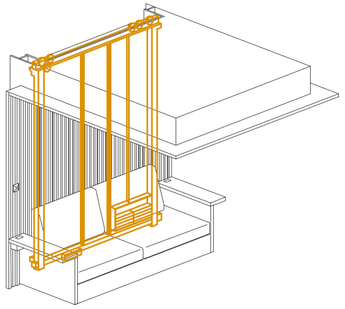


1 Cloudbed optie 1
Schaal: 1:50

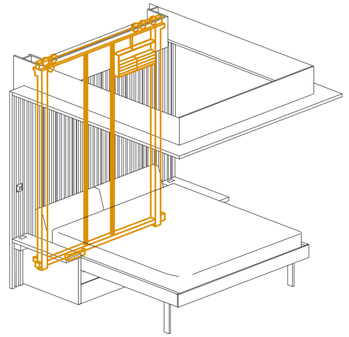


2 Cloudbed optie 2
Schaal: 1:50

Ontwerp en eigendom van Ori Living

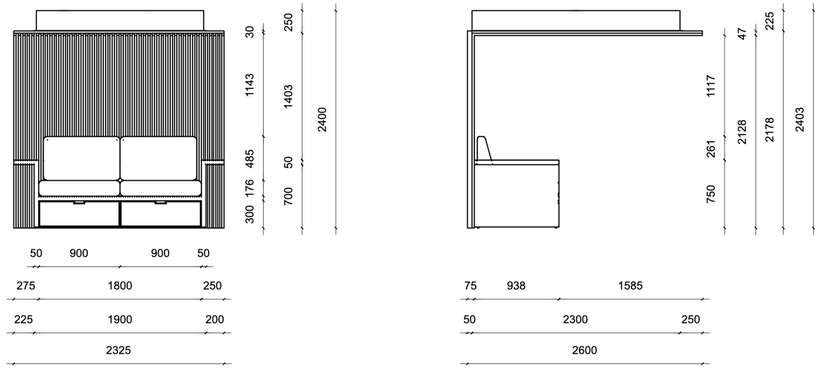


3 Cloudbed maatvoering optie 1
Schaal: 1:50

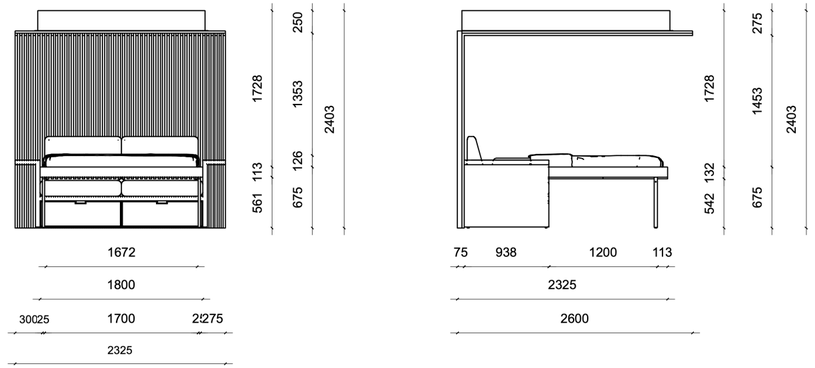


4 Cloudbed maatvoering optie 2
Schaal: 1:50


Ontwerp:	Ori Cloudbed
Ontwerper:	Ori Living
Opdrachtgever:	Minimal Design
Schaal:	1:50
Formaat:	A3
Eenheid:	mm
Datum:	15.06.2023
Tekening nr:	1

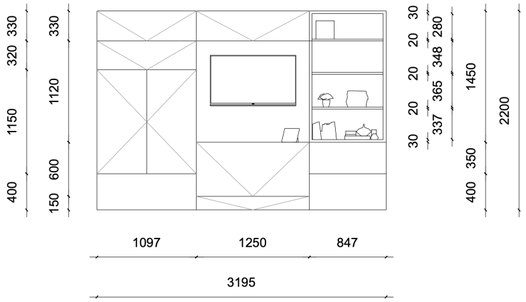


1 Maatvoering vooraanzicht
Schaal: 1:50

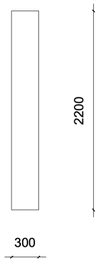


2 Maatvoering aanzicht rechts
Schaal: 1:50

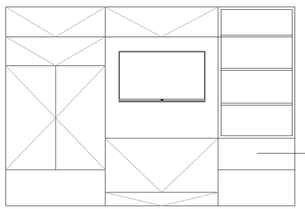


5 Materiaal
Schaal: 1:50

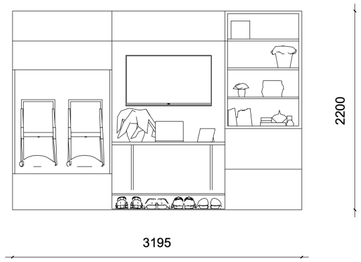

3 Maatvoering vooraanzicht 2
Schaal: 1:50

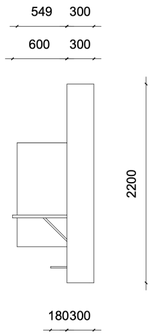


4 Maatvoering aanzicht rechts 2
Schaal: 1:50

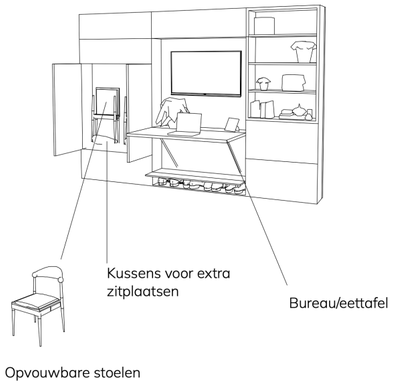


6 Aanwijzingen
Schaal: 1:50


Ontwerp:	Wandkast
Ontwerper:	Guusje Rozendom
Opdrachtgever:	Minimal Design
Schaal:	1:50
Formaat:	A3
Eenheid:	mm
Datum:	27.06.2023
Tekening nr:	1

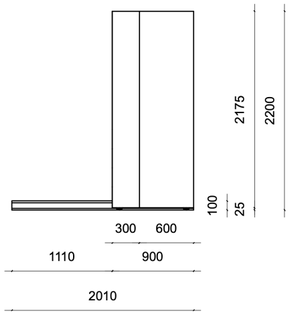


1 Kast vooraanzicht
Schaal: 1:50

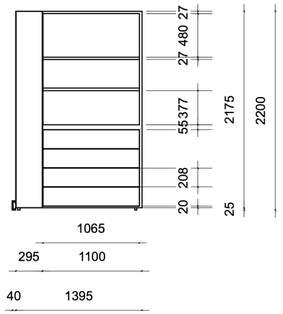


2 Kast aanzicht links
Schaal: 1:50

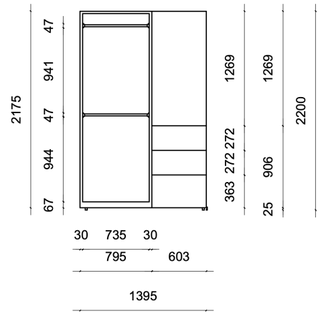


3 Kast aanzicht rechts
Schaal: 1:50

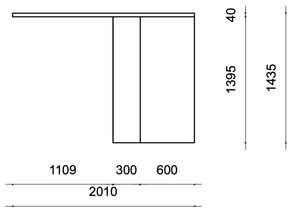


4 Kast bovenaanzicht
Schaal: 1:50

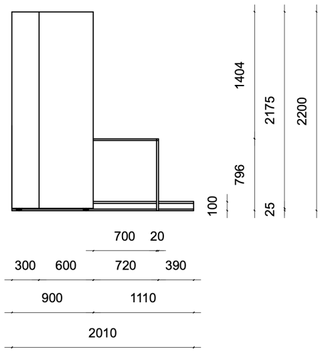


5 Kast + bureau vooraanzicht
Schaal: 1:50

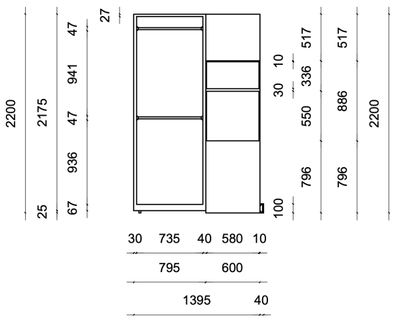


6 Kast + bureau aanzicht rechts
Schaal: 1:50

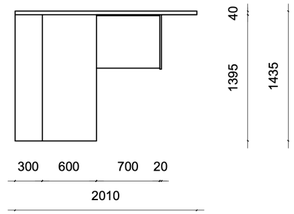

7 Kast + bureau bovenaanzicht
Schaal: 1:50

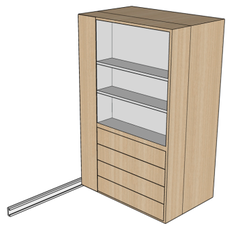

8 Iso kast
Schaal: 1:50

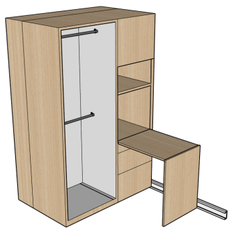

9 Iso kast + bureau
Schaal: 1:50


Ontwerp:	Verschuifbare kast
Ontwerper:	Guusje Rozendom
Opdrachtgever:	Minimal Design
Schaal:	1:50
Formaat:	A3
Eenheid:	mm
Datum:	20.06.2023
Tekening nr:	1

STUDIO 8


Ontwerp en eigendom van Ori Living




1 Aanzicht kast-onderstel
Schaal: 1:10

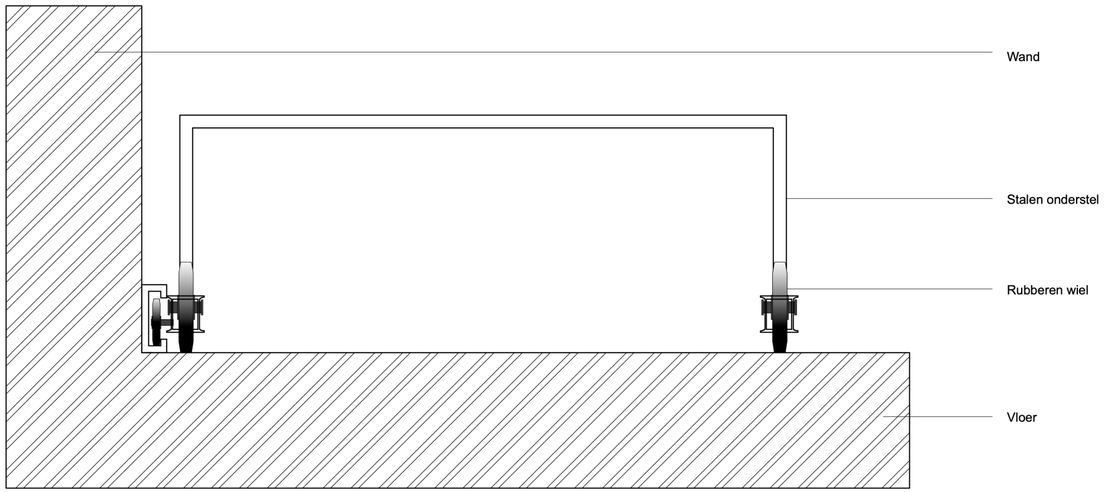

2 Lengte doorsnede AA kast-onderstel
Schaal: 1:10

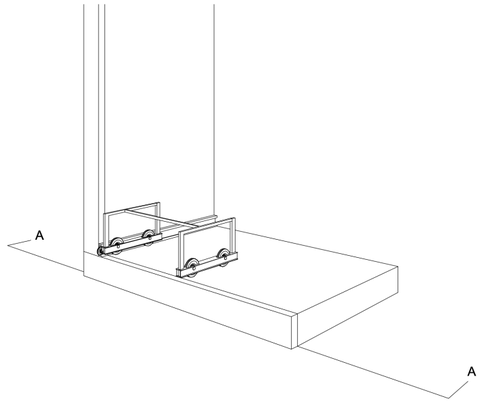


3 Aanzicht kast-onderstel
Schaal: 1:100

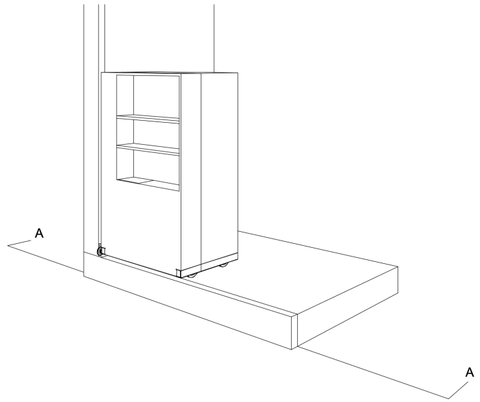


4 Aanzicht kast-onderstel met kast
Schaal: 1:100


Ontwerp:	Detail onderstel kast
Ontwerper:	Ori Living
Opdrachtgever:	Minimal Design
Schaal:	1:50
Formaat:	A3
Eenheid:	mm
Datum:	26.06.2023
Tekening nr:	1

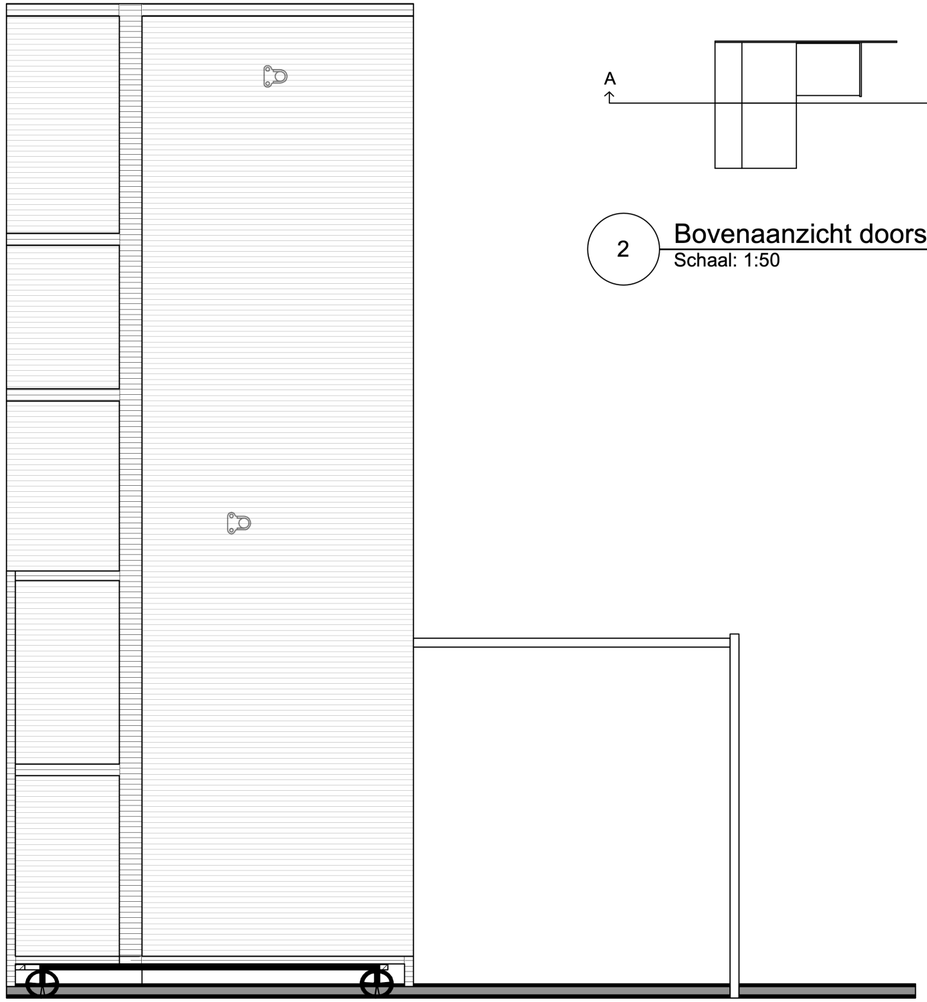

1 Doorsnede AA kast
Schaal: 1:10

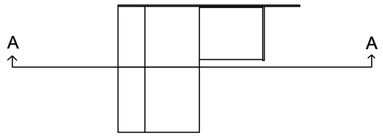


2 Bovenaanzicht doorsnede
Schaal: 1:50

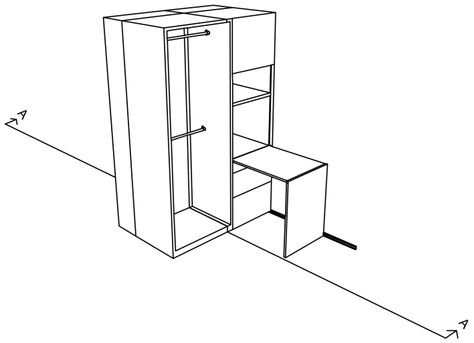


3 Iso beeld doorsnede
Schaal: 1:50

	Mdf-plaat, Pantoni hout Stabilo, 100% biobased populierenhout, PEFC gecertificeerd afgewerkt met decor Vicenza eik.


Ontwerp:	Doorsnede verschuifbare ka
Ontwerper:	Guusje Rozendom
Opdrachtgever:	Minimal Design
Schaal:	1:50
Formaat:	A3
Eenheid:	mm
Datum:	20.06.2023
Tekening nr:	2

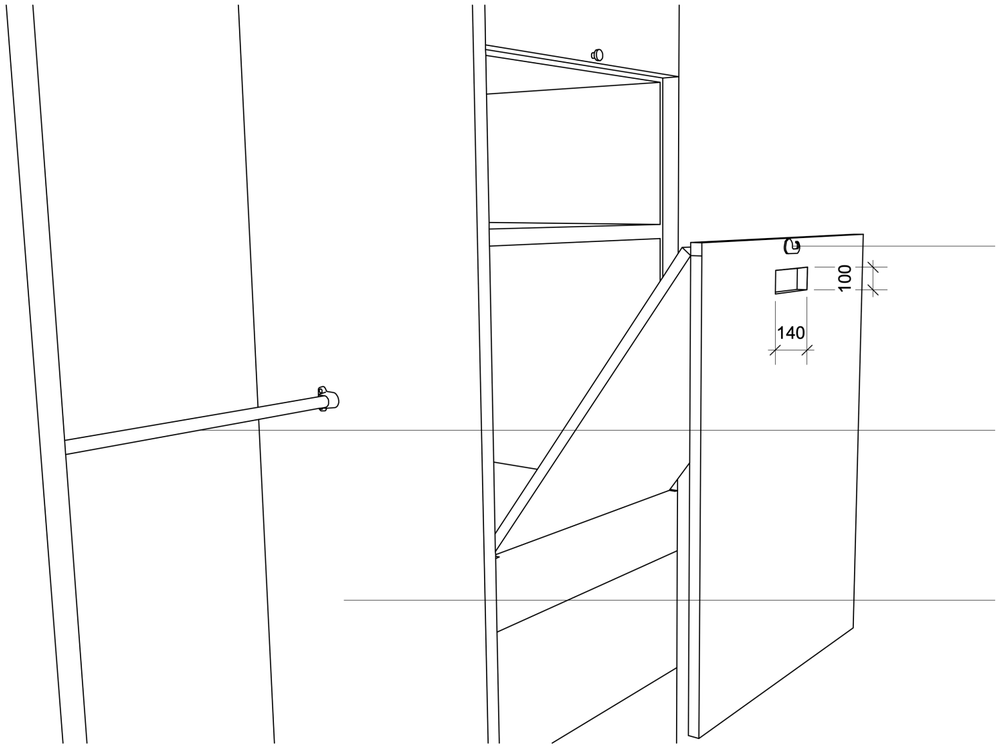


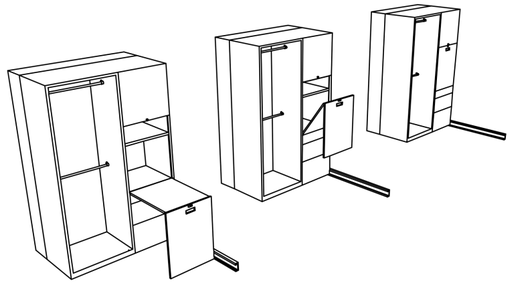

1 **Detail bureau uit kast**
Schaal: 1:20

Ontwerp:	Detail bureau uit kast
Ontwerper:	Guusje Rozendom
Opdrachtgever:	Minimal Design
Schaal:	1:50
Formaat:	A3
Eenheid:	mm
Datum:	20.06.2023
Tekening nr:	3

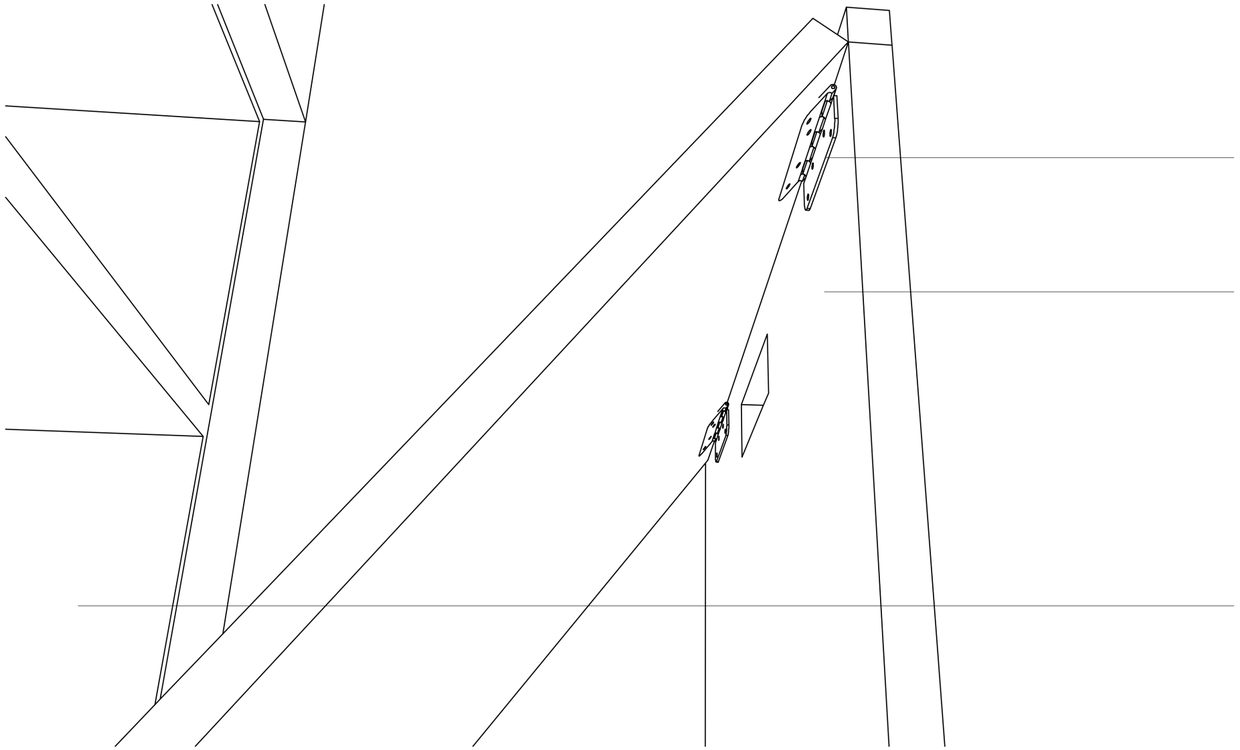

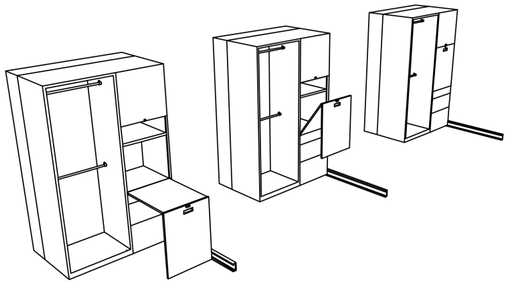

1 **Detail bureau uit kast**
Schaal: 1:20

Ontwerp:	Detail bureau uit kast
Ontwerper:	Guusje Rozendom
Opdrachtgever:	Minimal Design
Schaal:	1:50
Formaat:	A3
Eenheid:	mm
Datum:	20.06.2023
Tekening nr:	4

Bedankt voor uw aandacht en interesse

Mocht u nog vragen hebben over mijn ontwerp,
stuur gerust een mail naar:

499805@student.saxion.nl

Guusje Rozendom
499805
DDS3V.A4

Studio Semester, StuDio8

Studio 8

De getoonde afbeeldingen zijn sfeerbeelden en mogen niet als werktekening worden beschouwd. Kleuren, maten en structuren kunnen afwijken, graag bekijken wij deze met u samen aan de hand van echte kleurmonsters.